



RZUT PODSTAWOWY / ARANŻACJA / ZMIANY BUDOWLANE

ZESTAWIENIE POWIERZCHNI		
NR	NAZWA POMIESZCZENIA	POW. [M2]
0.1	KUCHNIA	14,55
LEGENDA		
	ŚCIANY ISTNIEJĄCE	
W	WENTYLACJA [KRATKA] ISTNIEJĄCA LUB PROJEKTOWANA	

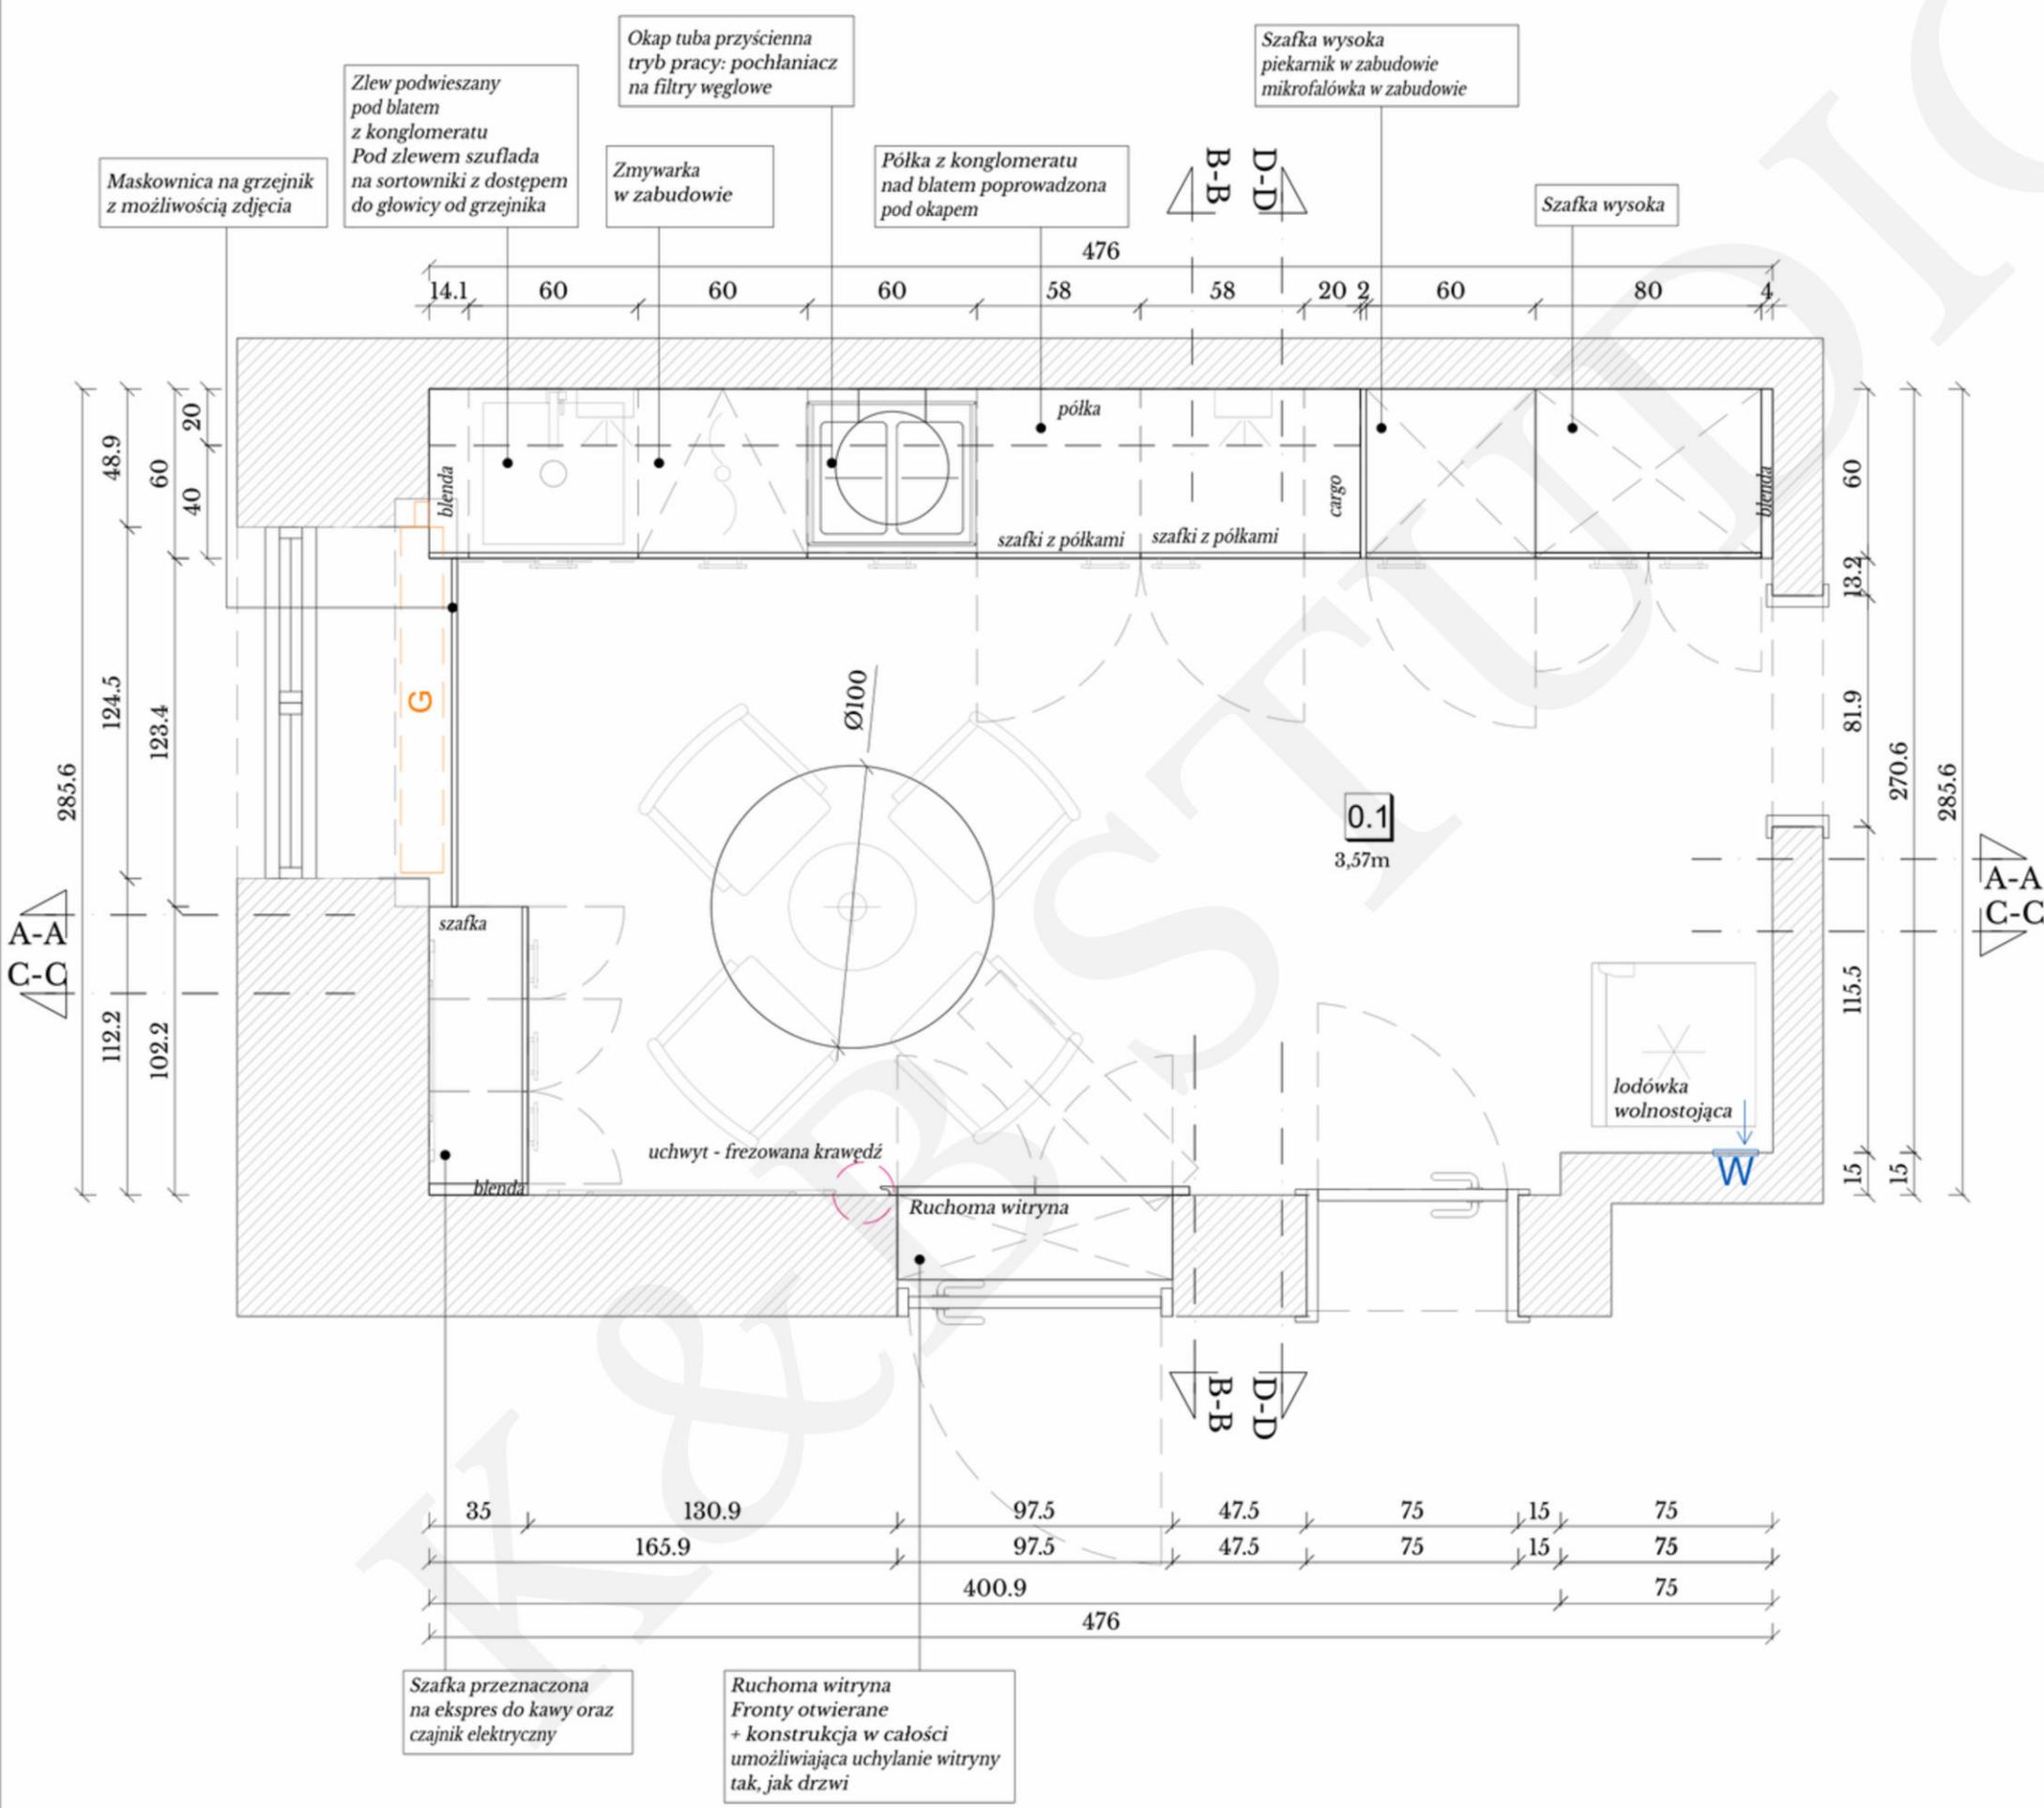

# RZUT PODSTAWOWY / ZMIANY BUDOWLANE

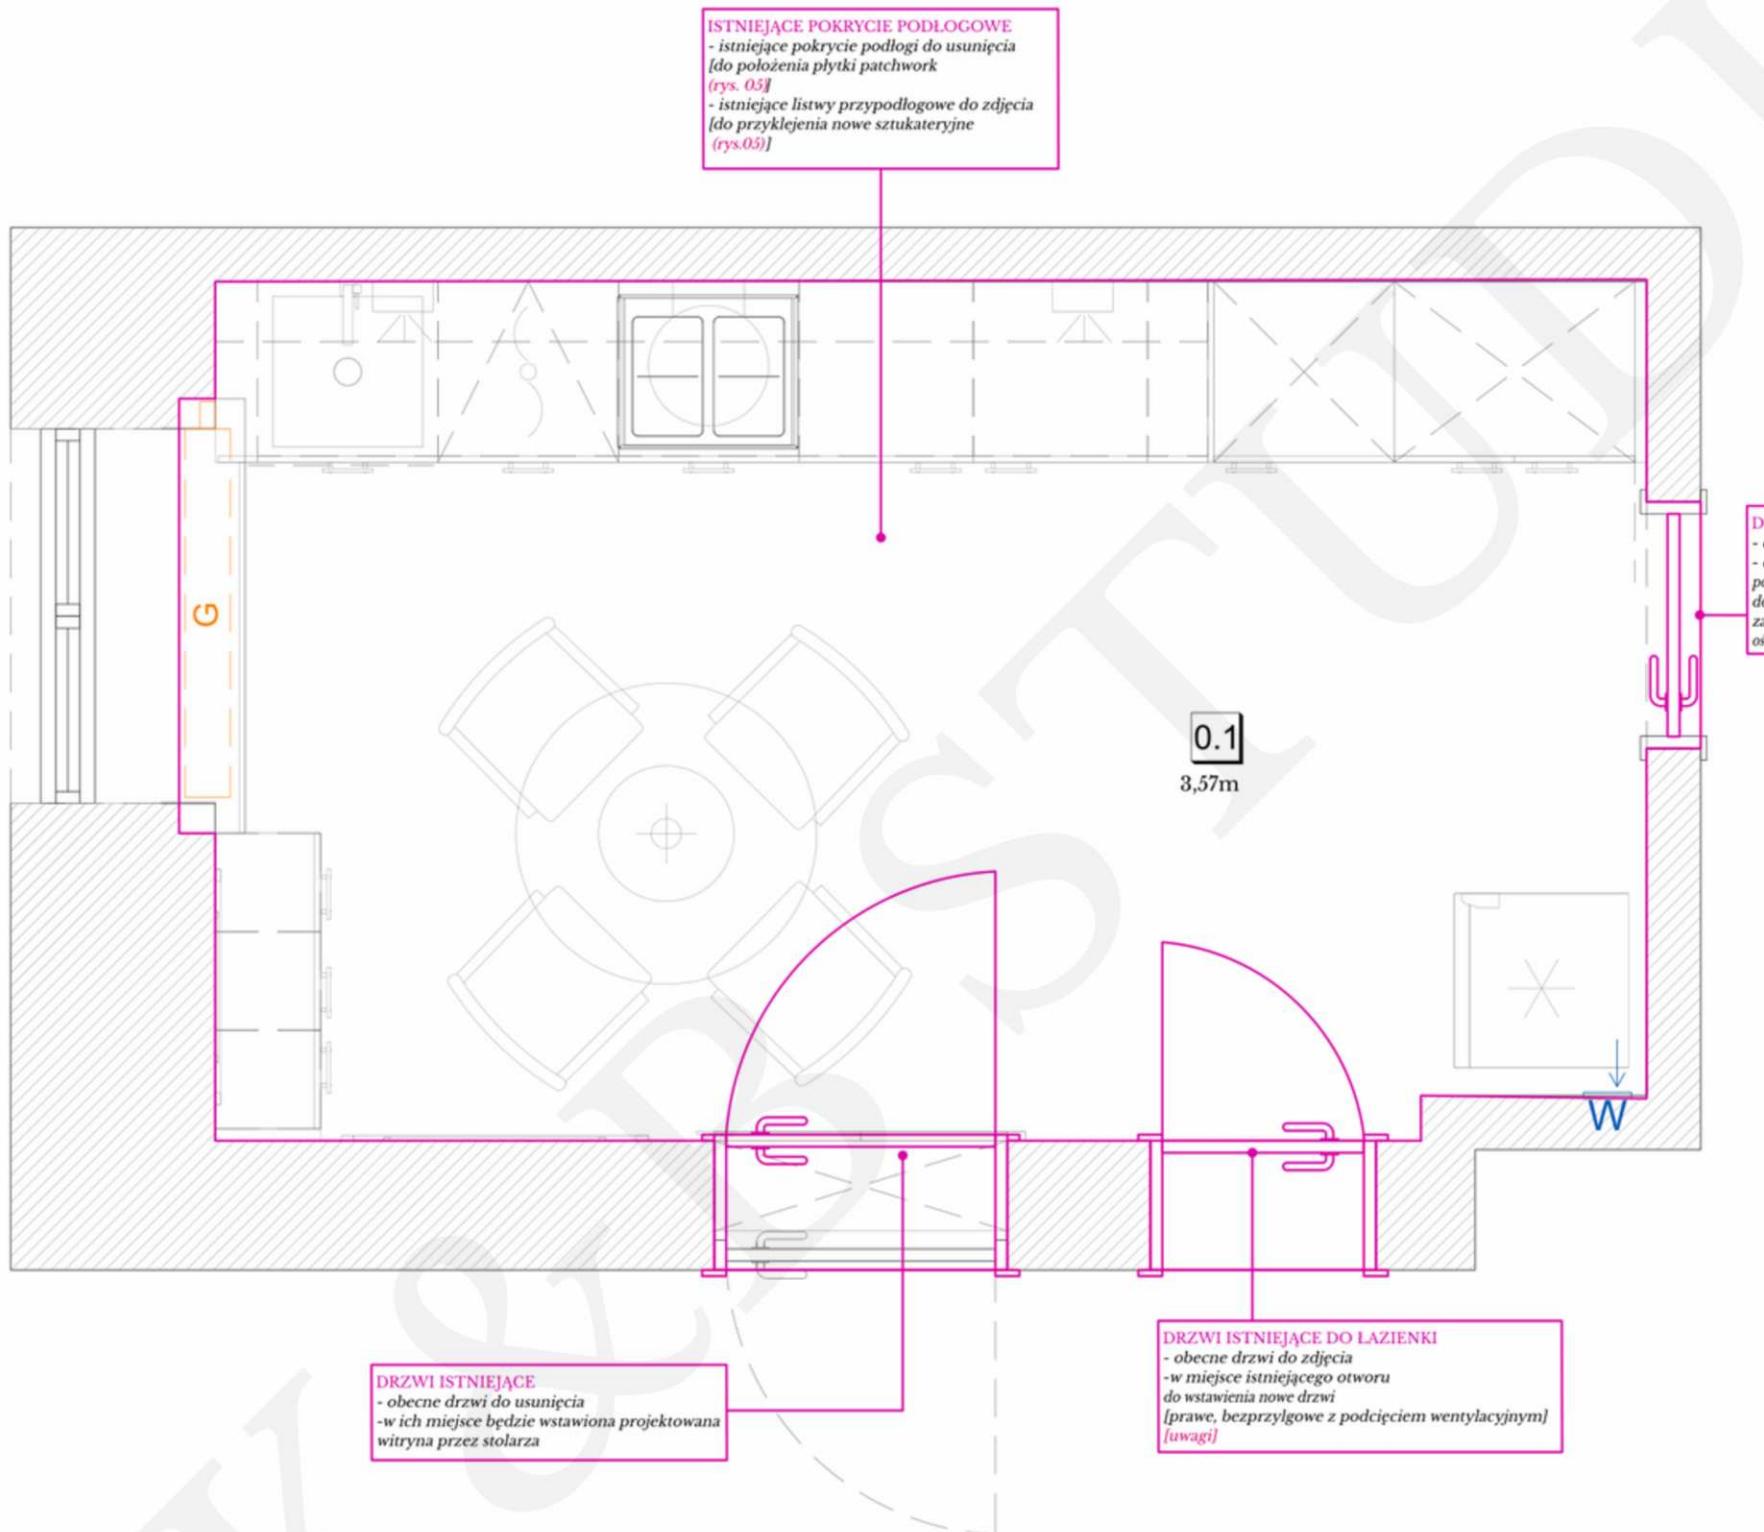

ZESTAWIENIE POWIERZCHNI		
NR	NAZWA POMIESZCZENIA	POW. [M <sup>2</sup> ]
0.1	KUCHNIA	14,55
<b>LEGENDA</b>		
	ŚCIANY ISTNIEJĄCE	
	ELEMENTY PROJEKTOWANE	
	ŚCIANY WYBURZENIA	
	SUFIT PODWIESZANY	
	SUFIT NAPINANY	
	NAWISY	
	SUCHA ZABUDOWA	
<b>W</b>	WENTYLACJA [KRATKA] ISTNIEJĄCA LUB PROJEKTOWANA	

## UWAGI

### drzwi do łazienki

PORTA ROYAL model A

- prawe bezprzylgowe
- z podcięciem wentylacyjnym [konieczność przy drzwiach do łazienki]
- klamka Bella Slim złota lub czarna [do wyboru przy zamawianiu drzwi]



## UWAGI PROJEKTOWE:

1. Przed przystąpieniem do prac należy dokładnie przejrzeć wszystkie rysunki i potwierdzić ich zgodność z Architektem i Inwestorem

2. Wymiary należy sprawdzić na budowie. W momencie wystąpienia widocznych różnic pomiędzy wymiarami na rysunkach, a w rzeczywistości należy skontaktować się z architektem.

Studio  
projektowania  
wnętrz



NAZWA INWESTYCJI:	PROJEKT KUCHNI Z JADALNIĄ	NUMER RYSUNKU:
ADRES INWESTYCJI:		SKALA RYSUNKU:
INWESTOR:	RZUT PODSTAWOWY ZMIANY BUDOWLANE	DATA OPRACOWANIA:
ARCHITEKT:	MGR INŻ. ARCH. KAROLINA PLECH TEL.: 696 850 891	PODPIS:

02

1:25

DATA:


26.02.2024r.

OPRACOWANIA:

26.02.2024r.

PODPIS:

# RZUT PODSTAWOWY / INSTALACJE ELEKTRYCZNE

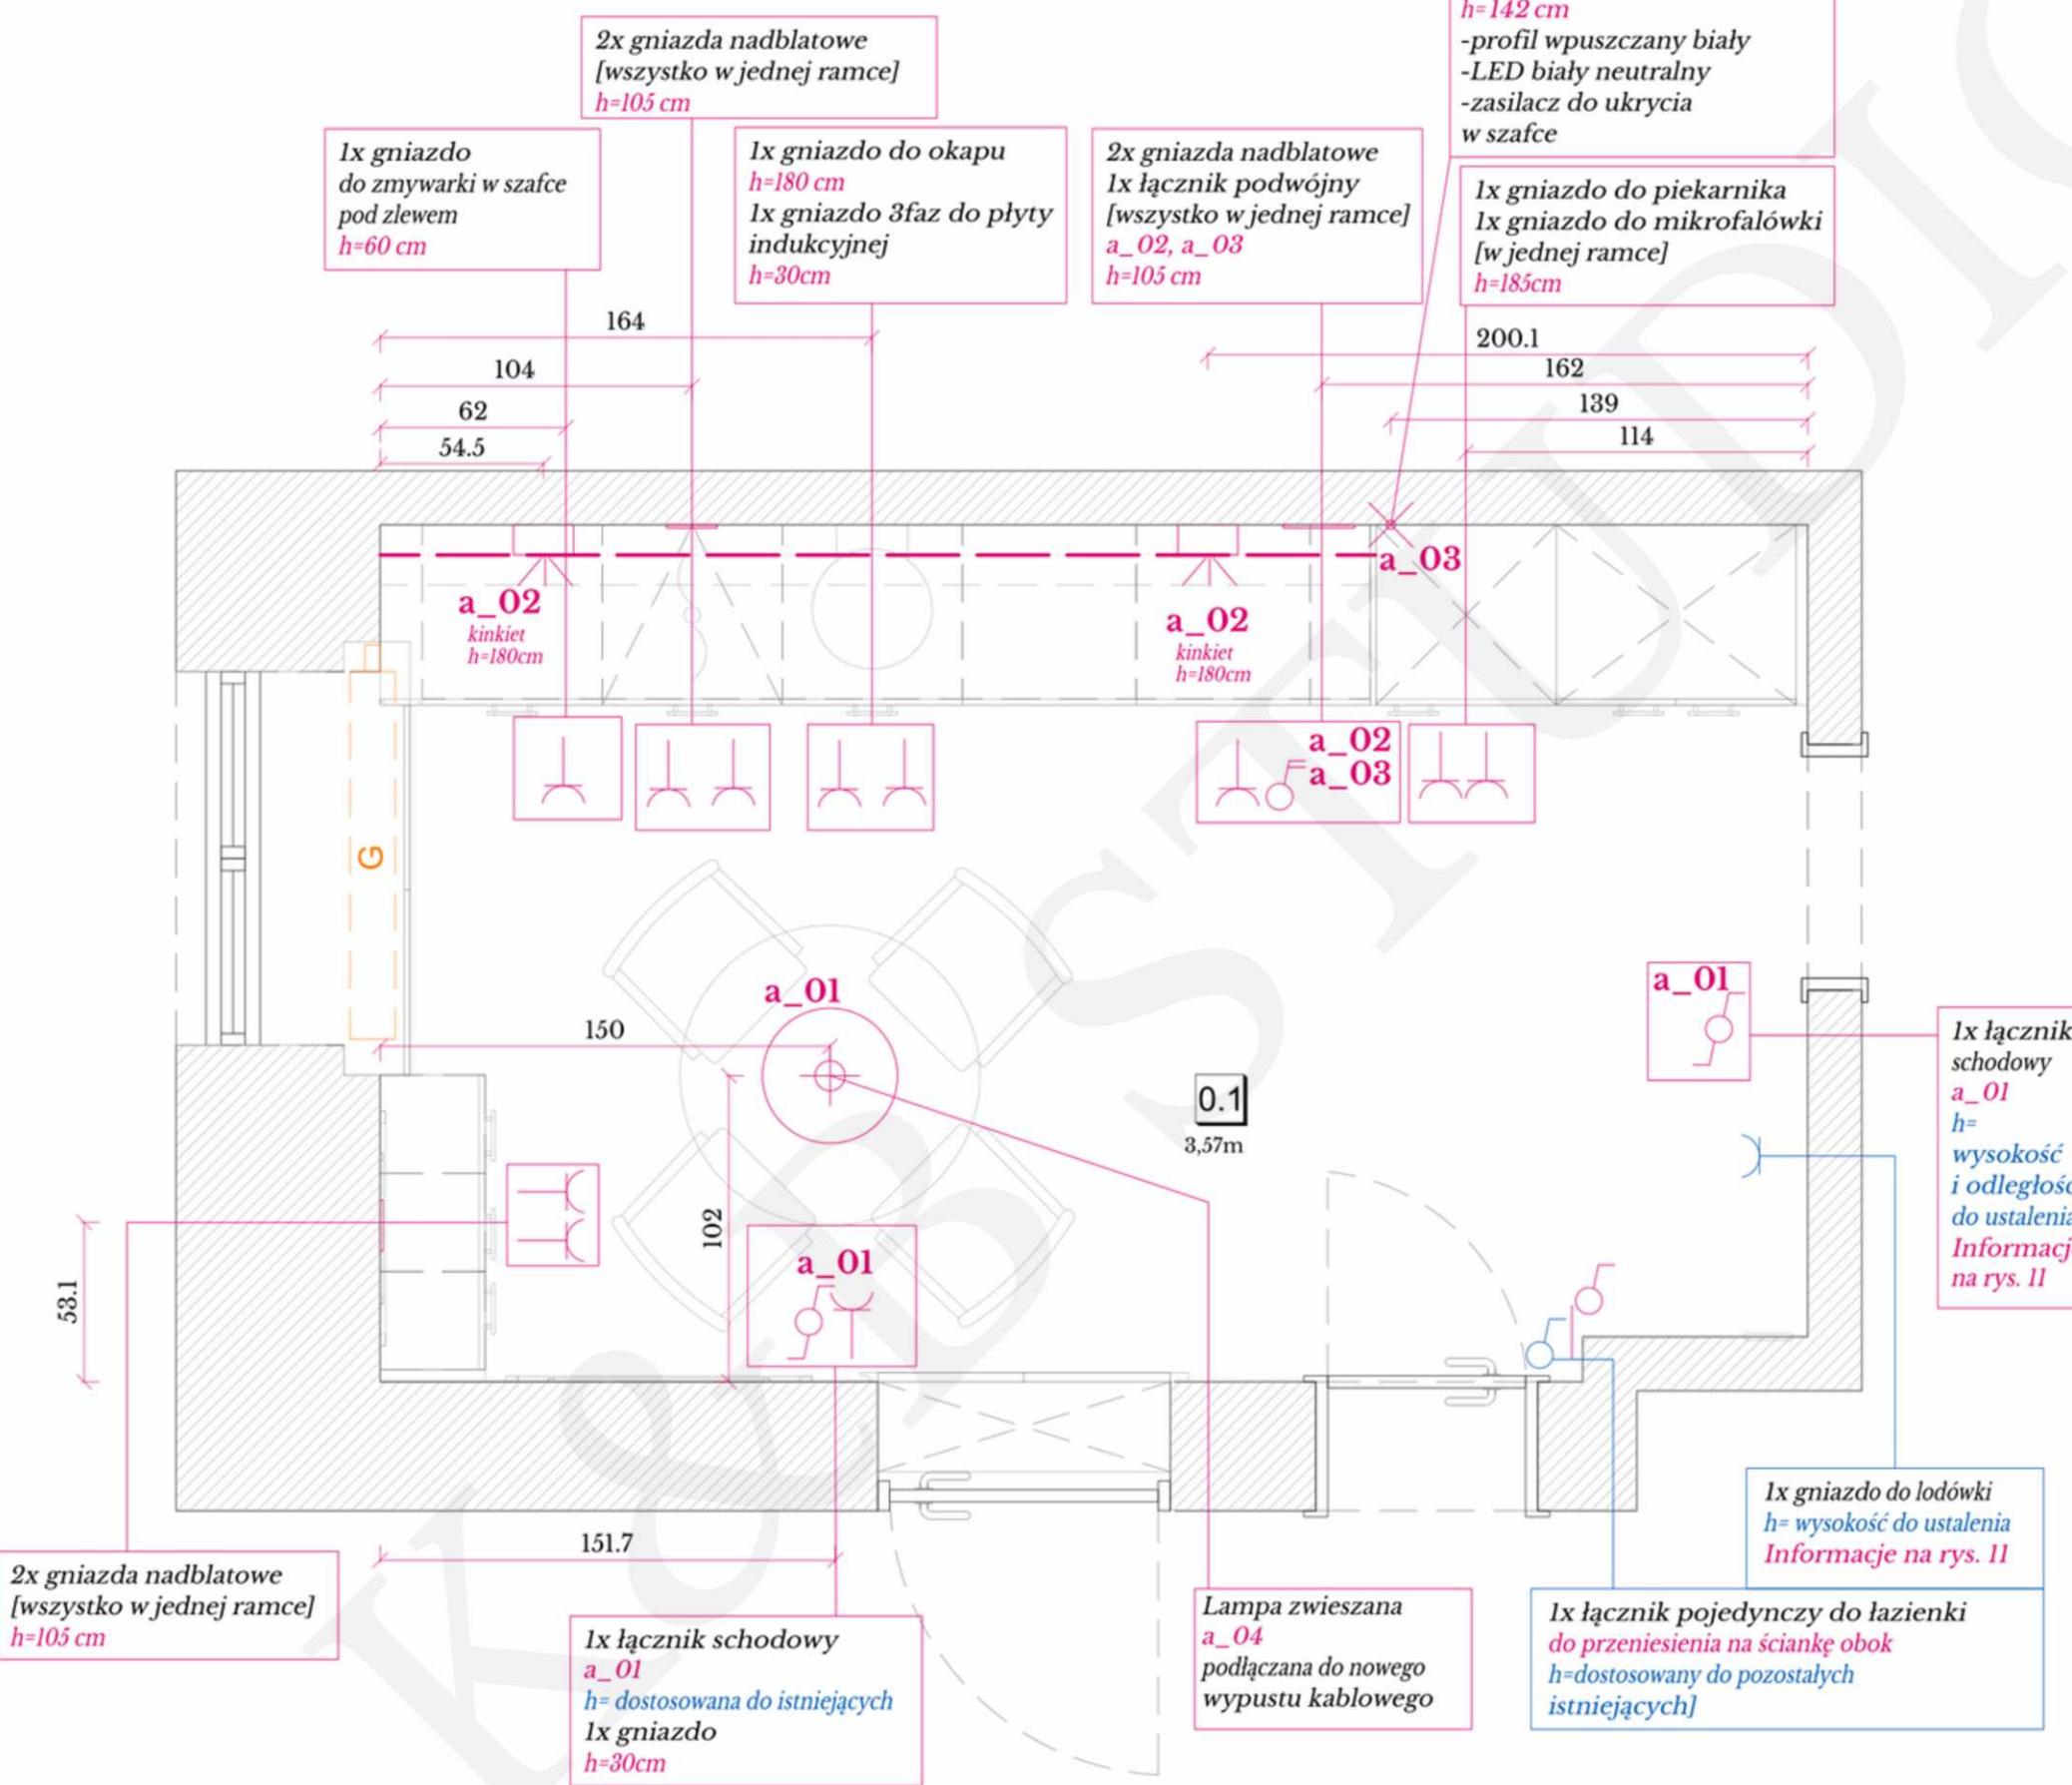

ZESTAWIENIE POWIERZCHNI		
NR	NAZWA POMIESZCZENIA	POW. [M <sup>2</sup> ]
0.1	KUCHNIA	14,55
LEGENDA		
ŚCIANY ISTNIEJĄCE		

**GNIAZDA PRĄDOWE I WŁĄCZNIKI**  
 -kolekcja Vectis Round  
 -kolor biały  
 -rodzaje ramek podane na rzucie obok




**UWAGI PROJEKTOWE:**  
 1. Przed przystąpieniem do prac należy dokładnie przejrzeć wszystkie rysunki i potwierdzić ich zgodność z Architektem i Inwestorem.  
 2. Wymiary należy sprawdzić na budowie. W momencie wystąpienia widocznych różnic pomiędzy wymiarami na rysunkach, a w rzeczywistości należy skontaktować się z architektem.

Studio projektowania wnętrz

**K&B**  
STUDIO

NAZWA INWESTYCJI:	PROJEKT KUCHNI Z JADALNIĄ	NUMER RYSUNKU: 03
ADRES INWESTYCJI:		SKALA RYSUNKU: 1:25
INWESTOR:	RZUTY PODSTAW. ARANŻACJA ZMIANY BUDOWLANE	DATA OPRACOWANIA: 26.02.2024r.
ARCHITEKT:	MGR INŻ. ARCH. KAROLINA PLECH TEL.: 696 850 891	PODPIS:

# RZUT PODSTAWOWY / INSTALACJE WOD KAN

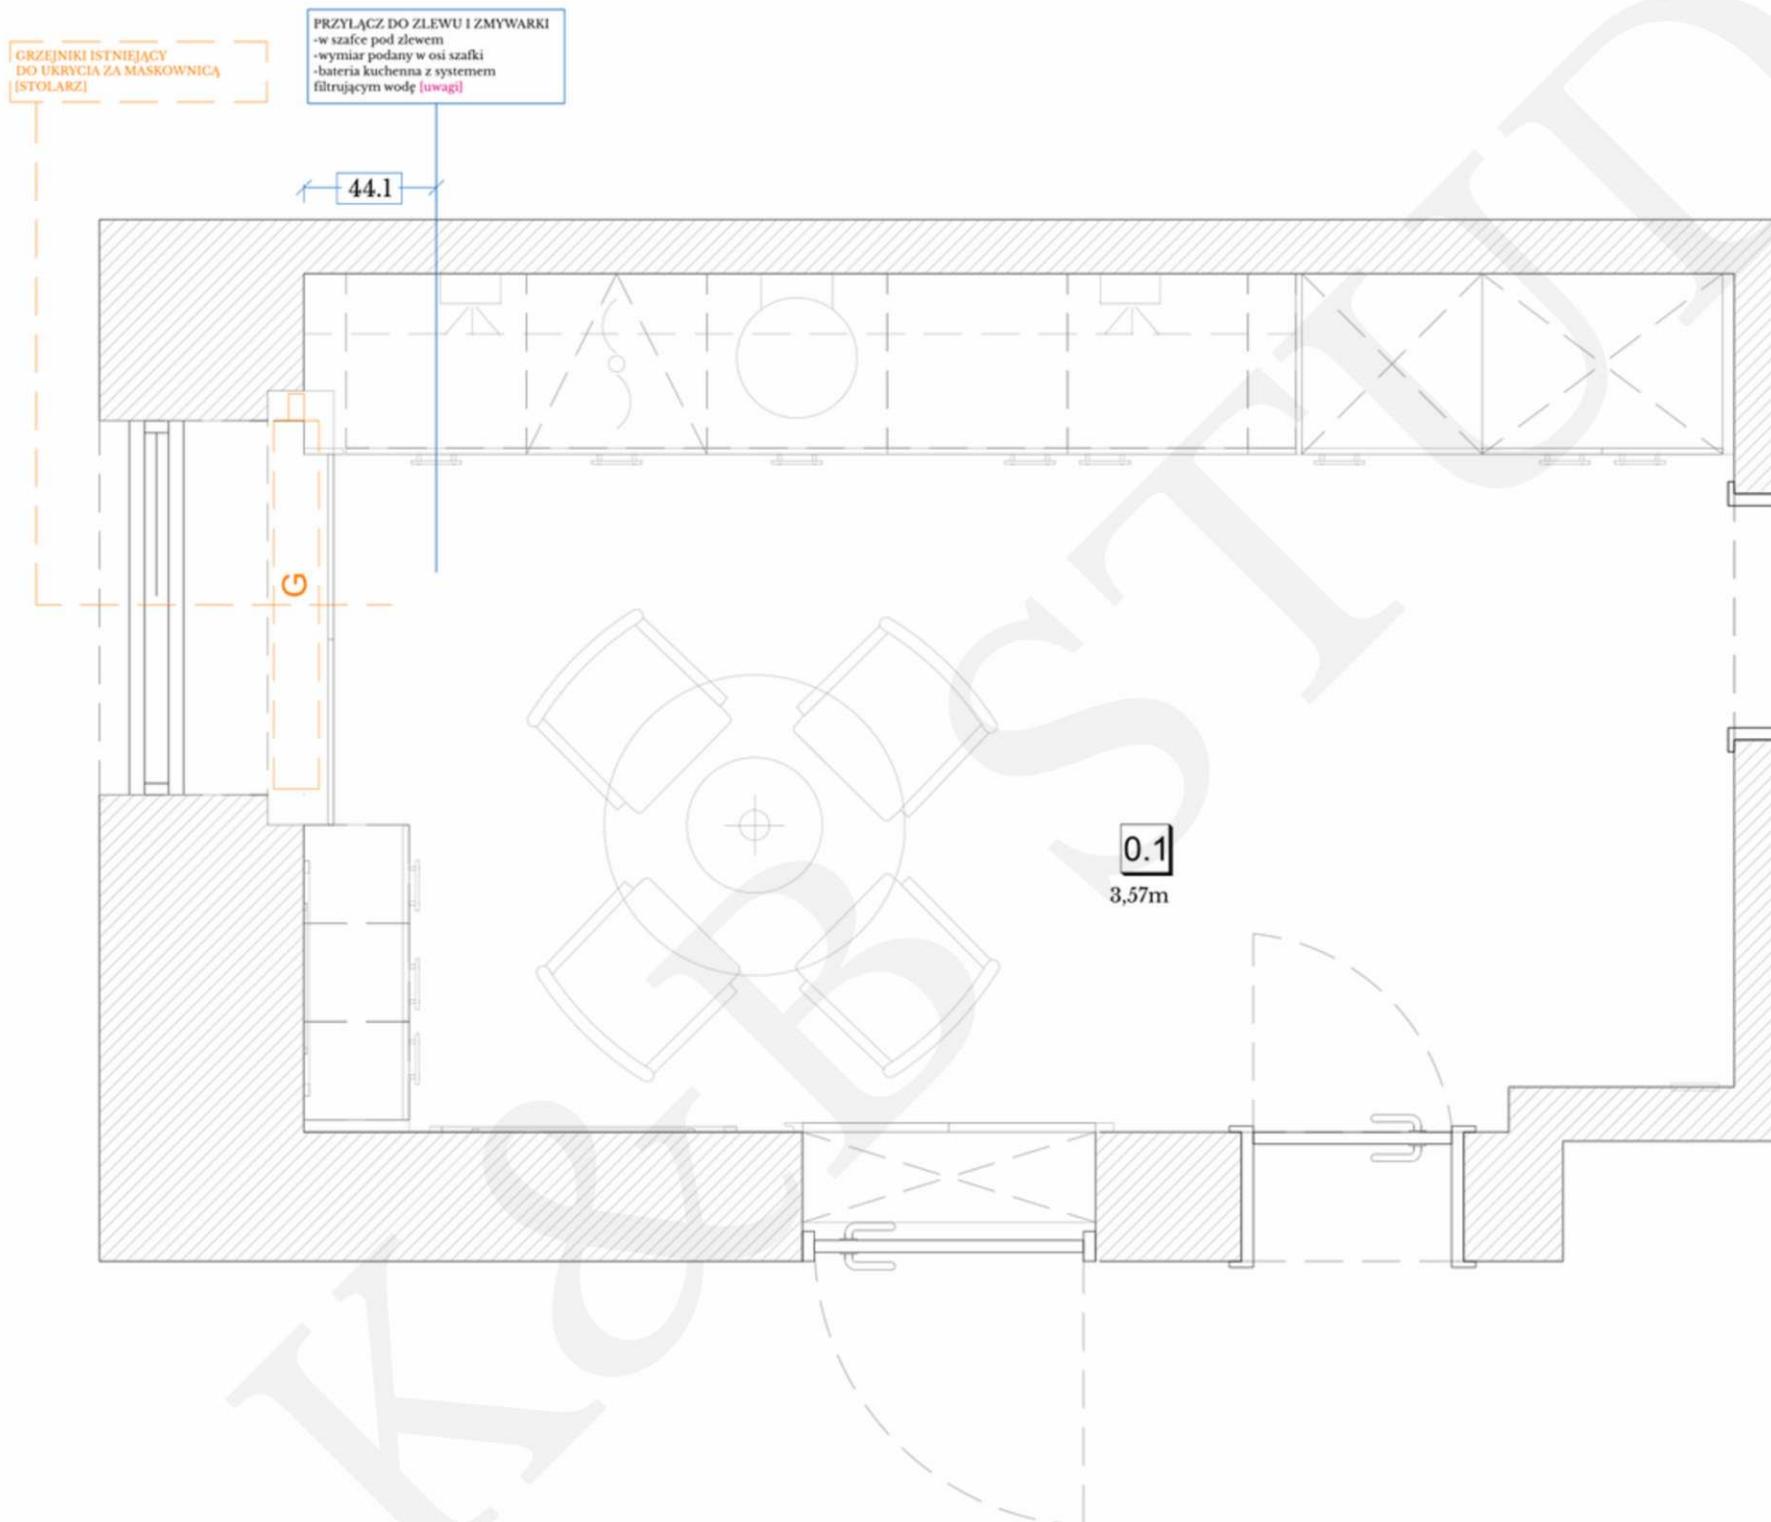

ZESTAWIENIE POWIERZCHNI		
NR	NAZWA POMIESZCZENIA	POW. [M <sup>2</sup> ]
0.1	KUCHNIA	14,55
LEGENDA		
		ŚCIANY ISTNIEJĄCE
		GRZEJNIK

## UWAGI

bateria kuchenna z systemem filtrującym

SWITCH Omnires

Bateria kuchenna z zestawem filtrującym

kolor: mosiądz szczotkowany [BSB]



## UWAGI PROJEKTOWE:

1. Przed przystąpieniem do prac należy dokładnie przejrzeć wszystkie rysunki i potwierdzić ich zgodność z Architektem i Inwestorem.

2. Wymiary należy sprawdzić na budowie. W momencie wystąpienia widocznych różnic pomiędzy wymiarami na rysunkach, a w rzeczywistości należy skontaktować się z architektem.

Studio  
projektowania  
wnętrz

**K**  
**D**  
S T U D I O


NAZWA INWESTYCJI:	PROJEKT KUCHNI Z JADALNIĄ	NUMER RYSUNKU:
ADRES INWESTYCJI:		SKALA RYSUNKU:
INWESTOR:	RZUT PODSTAWOWY INSTALACJE WOD KAN	DATA OPRACOWANIA:
ARCHITEKT:	MGR INŻ. ARCH. KAROLINA PLECH TEL.: 696 850 891	PODPIS:

04

1:25

26.02.2024r.

# RZUT PODSTAWOWY / WYKOŃCZENIE PODŁÓG

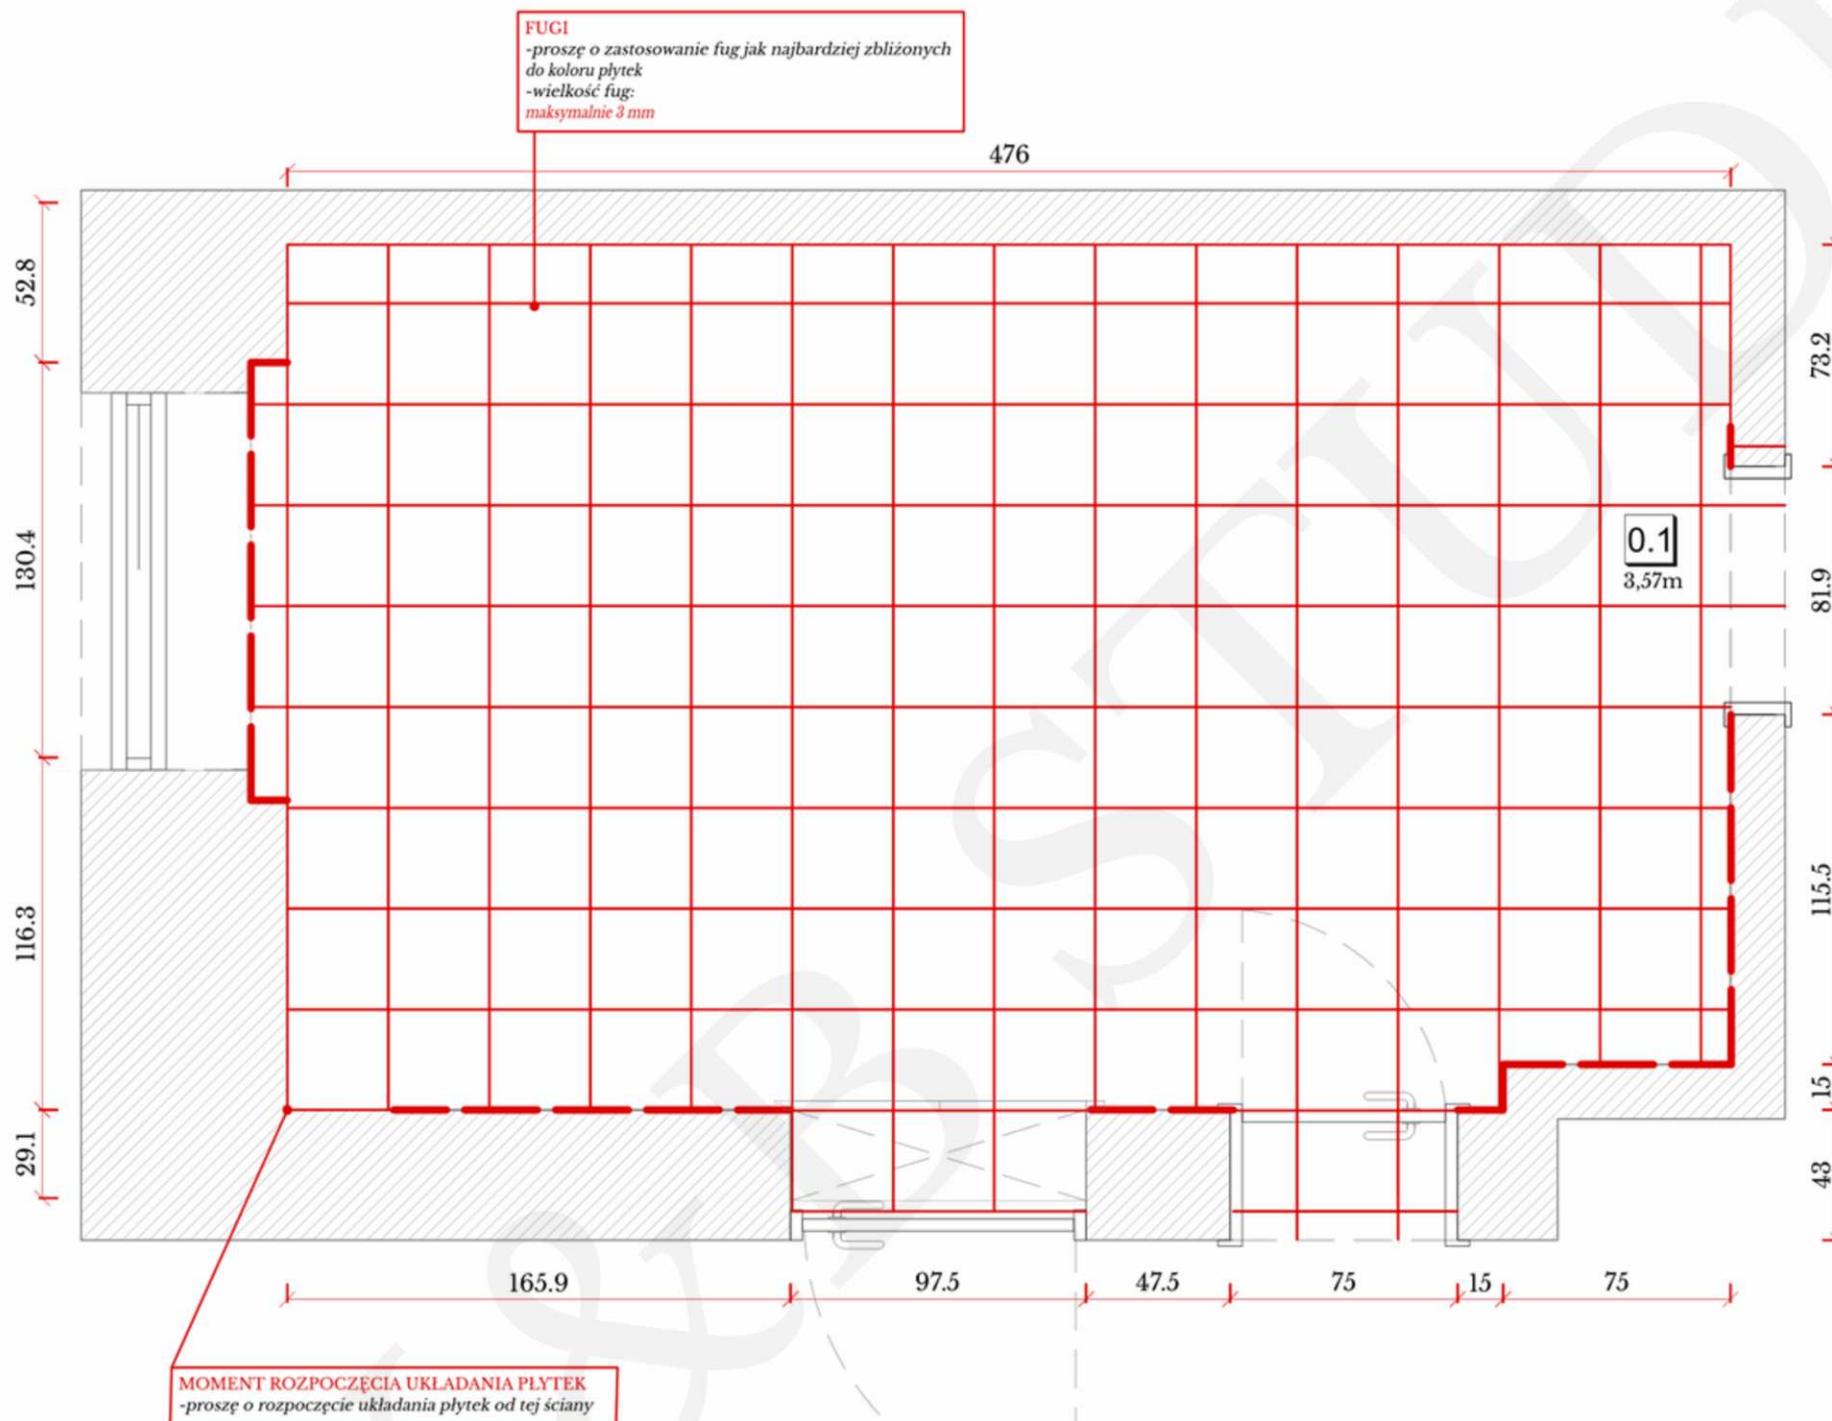

ZESTAWIENIE POWIERZCHNI		
NR	NAZWA POMIESZCZENIA	POW. [M <sup>2</sup> ]
0.1	KUCHNIA	14,55

## LEGENDA

	ŚCIANY ISTNIEJĄCE
--	-------------------

## LISTWA PRZYPODŁOGOWA

NR	MATERIAŁY	UKŁADANIE	ILOŚĆ
1	PLYTki PODŁOGOWE PATCHWORK OKTAGONALNE -terakota Oxford Negro 33,3x33,3cm gr. 9 mm Realonda Ceramica	WEDŁUG UKŁADU POKAZANEGO NA RYSUNKU OBOK	ok. 14,25 m <sup>2</sup> + proszę o doliczenie 10% zapasu
2	LISTWA PRZYPODŁOGOWA -MD094 Mardom Decor wys.9,4 cm	WEDŁUG UKŁADU POKAZANEGO NA RYSUNKU OBOK	ok. 5,82 mb + proszę o doliczenie 10% zapasu

## UWAGA

- ilości podane powyżej do sprawdzenia przez wykonawców przed zamówieniem produktów

## UWAGI PROJEKTOWE:

- Przed przystąpieniem do prac należy dokładnie przejrzeć wszystkie rysunki i potwierdzić ich zgodność z Architektem i Inwestorem
- Wymiary należy sprawdzić na budowie. W momencie wystąpienia widocznych różnic pomiędzy wymiarami na rysunkach, a w rzeczywistości należy skontaktować się z architektem.


Studio  
projektowania  
wnętrz



NAZWA INWESTYCJI:	PROJEKT KUCHNI Z JADALNIĄ	NUMER RYSUNKU:
ADRES INWESTYCJI:		SKALA RYSUNKU:
INWESTOR:	RZUT PODSTAWOWY WYKOŃCZENIE PODŁOG	DATA OPRAWOWANIA:
ARCHITEKT:	MGR INŻ. ARCH. KAROLINA PLECH TEL.: 696 850 891	PODPIS:
		26.02.2024r.

## RZUT PODSTAWOWY / WYKOŃCZENIE ŚCIAN

## SZTUKATERIA NA ŚCIANIE Z ZABUDOWĄ KUCHENNĄ [PRZEKRÓJ]

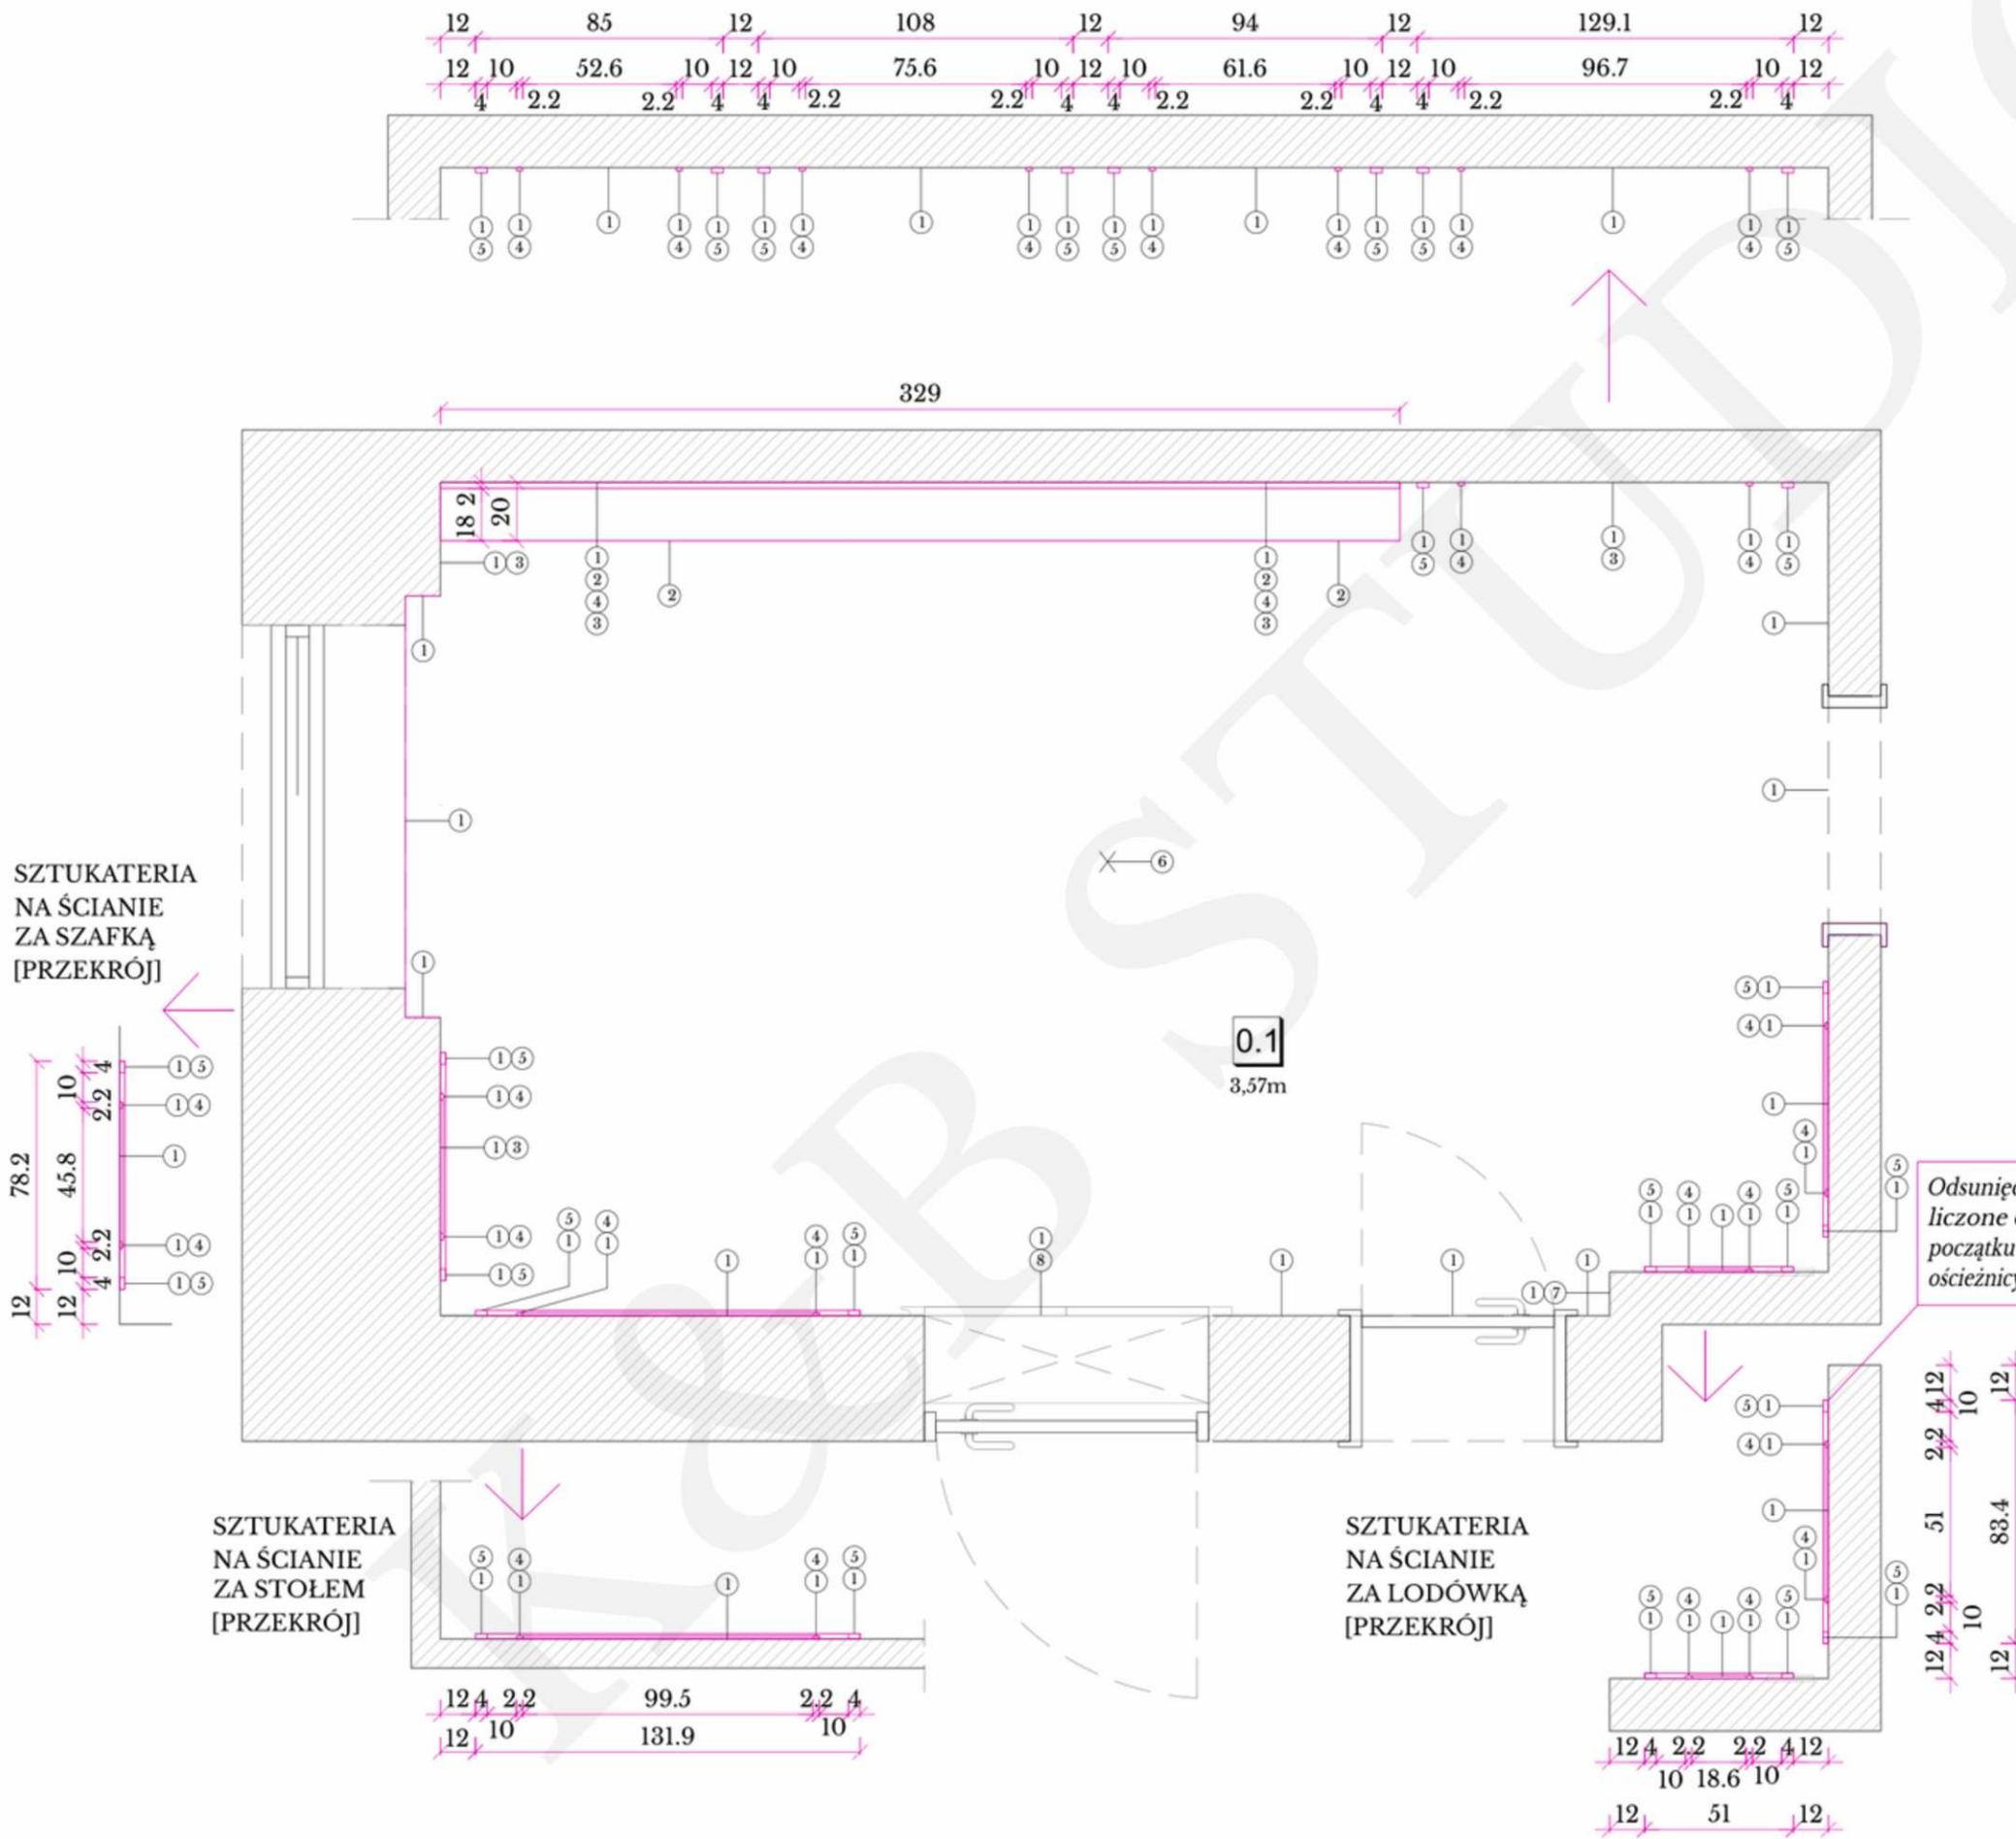

ZESTAWIENIE POWIERZCHNI			
NR	NAZWA POMIESZCZENIA	POW. [M2]	
0.1	KUCHNIA	14,55	
LEGENDA			
	ŚCIANY ISTNIEJĄCE		
W	WENTYLACJA [KRATKA] ISTNIEJĄCA LUB PROJEKTOWANA		
	ELEMENTY ŚCIENNE DO PRZYKLEJENIA / ZAMOCOWANIA		
NR	NAZWA	NR	NAZWA
1	FARBA BIAŁA	3	ZABUDOWA MEBLOWA STOLARZ <i>[dokładne informacje na rysunkach]</i>
2	KONGLOMERAT GR. 2 CM [OPASKA NAD BLATEM]		
4	SZTUKATERIA MD003 z polimeru HD 2.2 x 1 x 200 cm [Mardom Decor]	5	SZTUKATERIA MD002 z polimeru HD 4 x 1.8 x 200 cm [Mardom Decor]
6	SUFIT FARBA BIAŁA		

#### **UWAGI PROJEKTOWE:**

1. Przed przystąpieniem do prac należy dokładnie przejrzeć wszystkie rysunki i potwierdzić ich zgodność z Architektem i Inwestorem
  2. Wymiary należy sprawdzić na budowie. W momencie wystąpienia widocznych różnic pomiędzy wymiarami na rysunkach, a w rzeczywistości należy skontaktować się z architektem.


Studio  
projektowania  
wnętrz



NAZWA INWESTYCJI:	PROJEKT KUCHNI Z JADALNIĄ	NUMER RYSUNKU: <b>06</b>
ADRES INWESTYCJI:		SKALA RYSUNKU: <b>1:25</b>
INWESTOR:	RZUT PODSTAWOWY WYKOŃCZENIE ŚCIAN	DATA OPRACOWANIA: <b>26.02.2024r.</b>
ARCHITEKT:	MGR INŻ. ARCH. KAROLINA PLECH TEL.: 696 850 891	PODPIS:

# PRZEKROJE / ARANŻACJA

## PRZEKRÓJ A-A

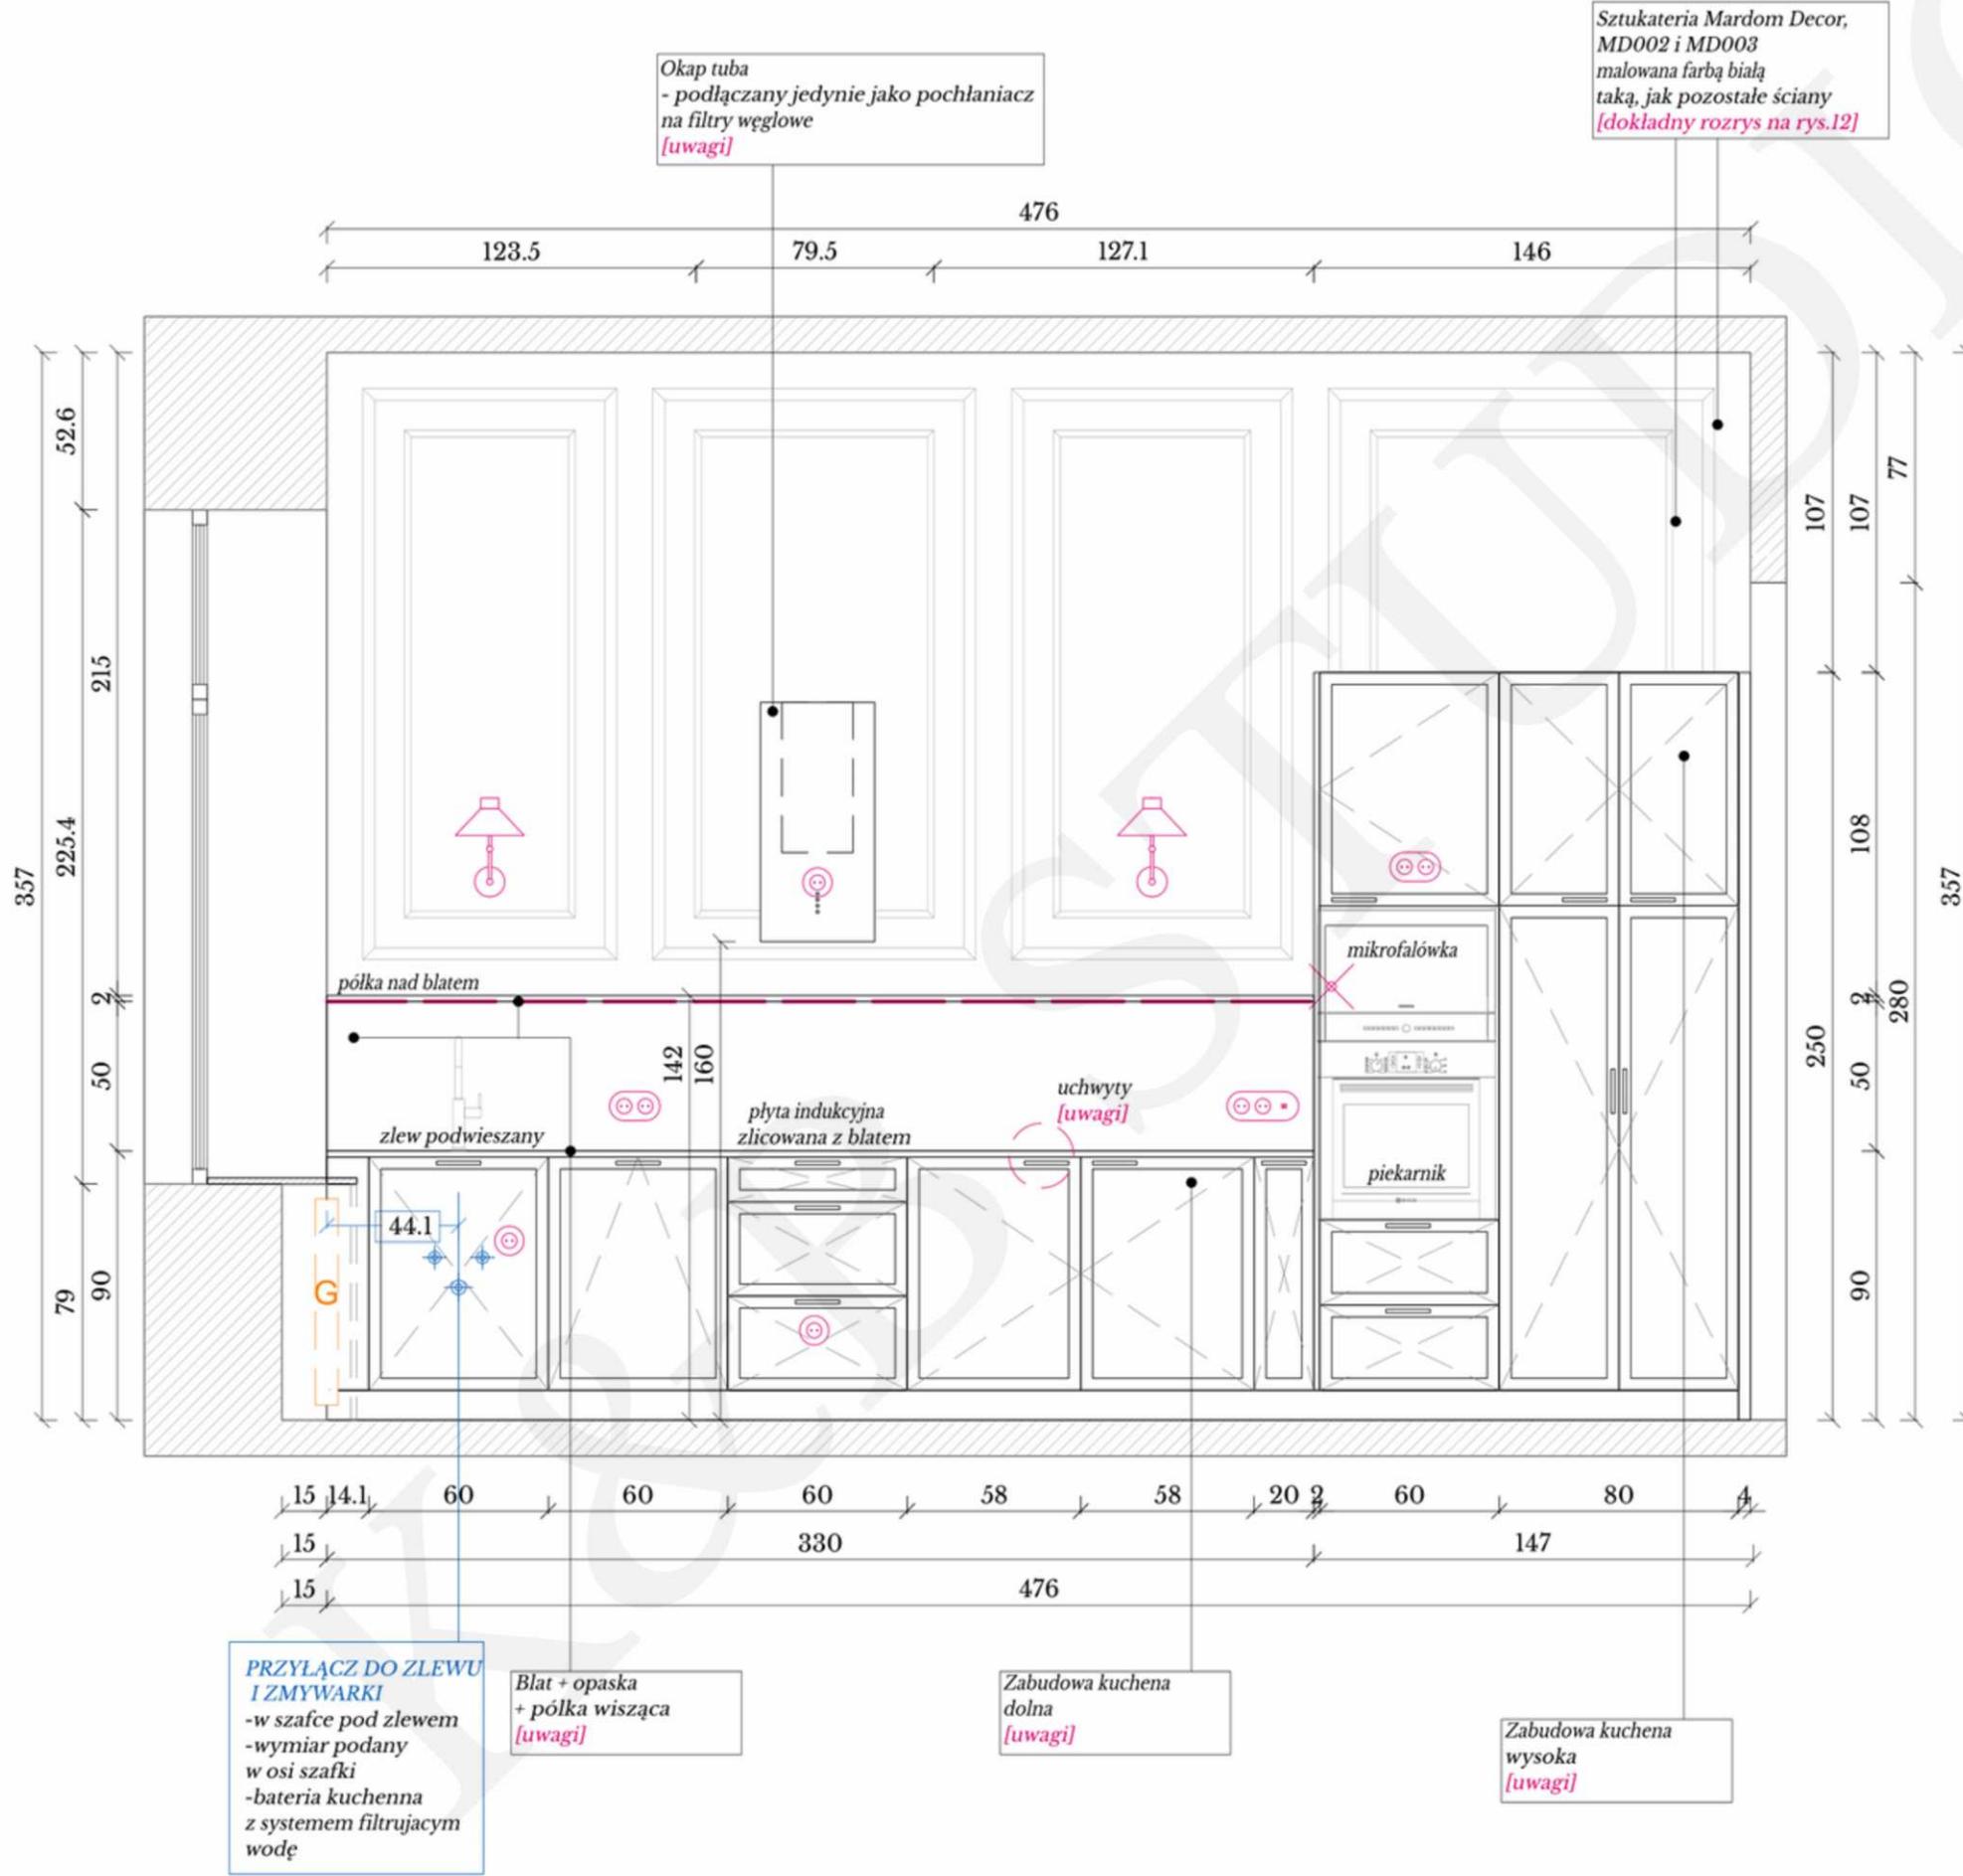


## LEGENDA

ŚCIANY ISTNIEJĄCE

## MATERIAŁY [UWAGI]

**BLAT + OPASKA NAD BLATEM + PÓŁKA**  
konglomerat kwarcowy  
Bronze Coast lub Calacatta Volegno  
gr. 2 cm  
TechniStone

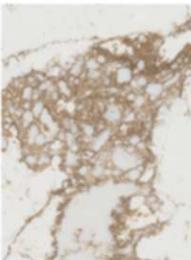

## FRONTY + WNĘTRZE

fronty frezowane - ramka 4 cm  
lakier granatowy mat RAL 5000 lub RAL 5013 lub RAL 5026  
[proszę o przygotowanie próbek frontów do powyższych kolorów]

wnętrze  
płyta laminowana dobrana pod kolor wybranego koloru frontu

**SZUFLADY SYSTEM**  
antaro BLUM




## UCHWYTY

**Uchwyty RELING MOSIĘŻNY**  
rozstaw: 128mm  
Hvyt

## OKAP TUBA PRZYŚCIENNA

**TUBUS**  
tryb pracy - pochłaniac z filtrem węglowym  
kolor: Gold Steel

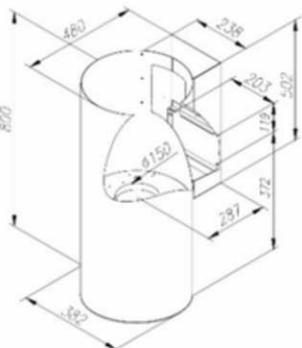

CIARKO

## UWAGI PROJEKTOWE:

- Przed przystąpieniem do prac należy dokładnie przejrzeć wszystkie rysunki i potwierdzić ich zgodność z Architektem i Inwestorem
- Wymiary należy sprawdzić na budowie. W momencie wystąpienia widocznych różnic pomiędzy wymiarami na rysunkach, a w rzeczywistości należy skontaktować się z architektem.


Studio projektowania wnętrz



NAZWA INWESTYCJI:	PROJEKT KUCHNI Z JADALNIĄ	NUMER RYSUNKU:
ADRES INWESTYCJI:		SKALA RYSUNKU:
INWESTOR:		1:25
ARCHITEKT:	MGR INŻ. ARCH. KAROLINA PLECH TEL.: 696 850 891	DATA OPRACOWANIA: 26.02.2024r.
		PODPIS:

# PRZEKROJE /INSTALACJE ELEKTRYCZNE


## PRZEKRÓJ A-A

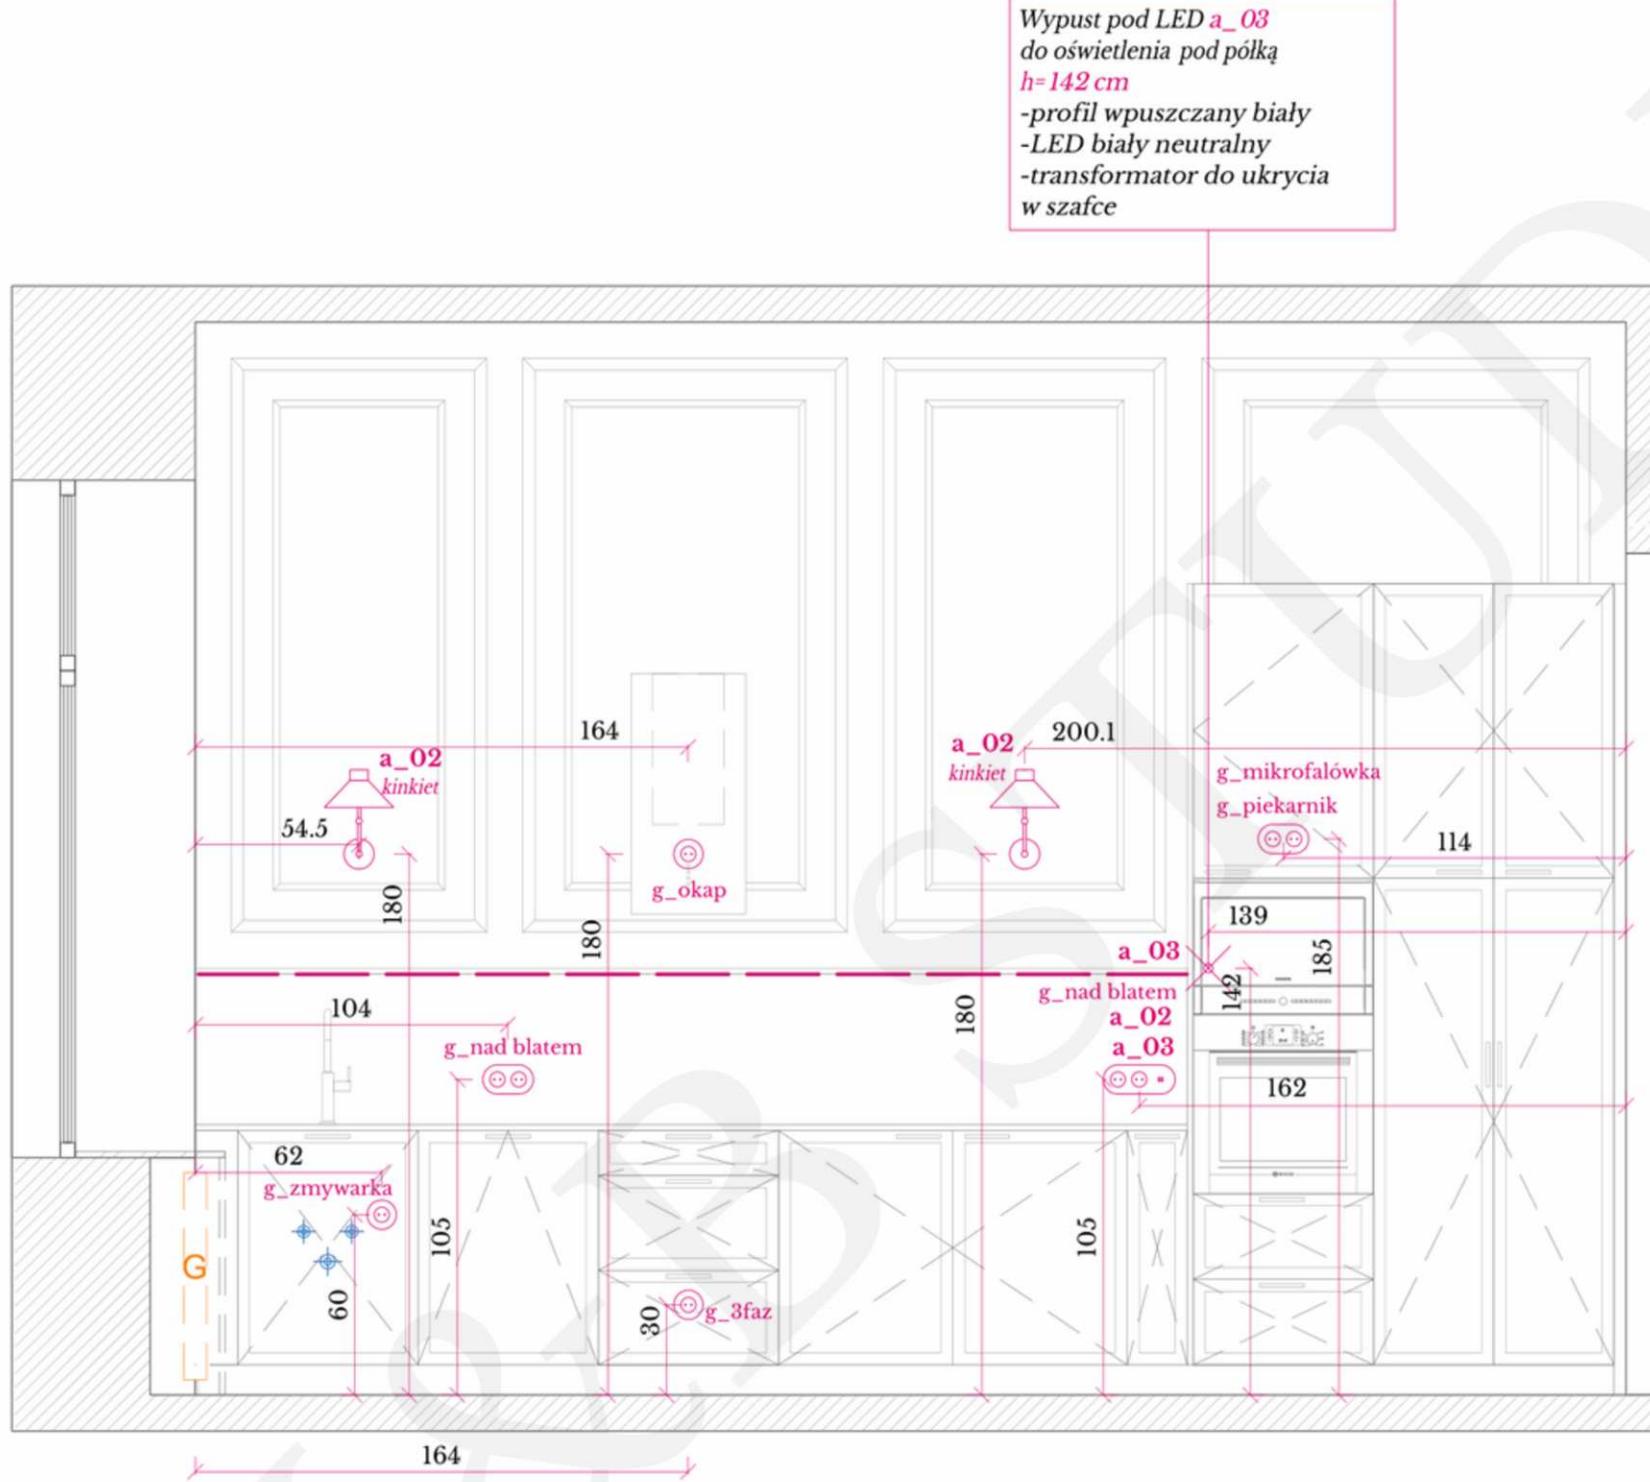

LEGENDA	
	ŚCIANY ISTNIEJĄCE
<b>GNIAZDA PRĄDOWE I WŁĄCZNIKI</b>	
-kolekcja Vectis Round	
-kolor biały	
-rodzaje ramek podane na rzucie obok	
<b>UWAGI PROJEKTOWE:</b>	
1.Pzed przystąpieniem do prac nalezy dokładnie przejrzeć wszystkie rysunki i potwierdzić ich zgodność z Architektem i Inwestorem	
2.Wymiary należy sprawdzić na budowie. W momencie wystąpienia widocznych różnic pomiędzy wymiarami na rysunkach, a w rzeczywistości nalezy skontaktować się z architektem.	
<b>Studio projektowania wnętrz</b> 	
NAZWA INWESTYCJI:	PROJEKT KUCHNI Z JADALNIĄ
ADRES INWESTYCJI:	SKALA RYSUNKU: <b>08</b>
INWESTOR:	DATA OPRACOWANIA: <b>1:25</b> <b>26.02.2024r.</b>
ARCHITEKT:	MGR INŻ. ARCH. KAROLINA PLECH TEL.: 696 850 891
	PODPIS:


# PRZEKROJE / ARANŻACJA

## PRZEKRÓJ B-B

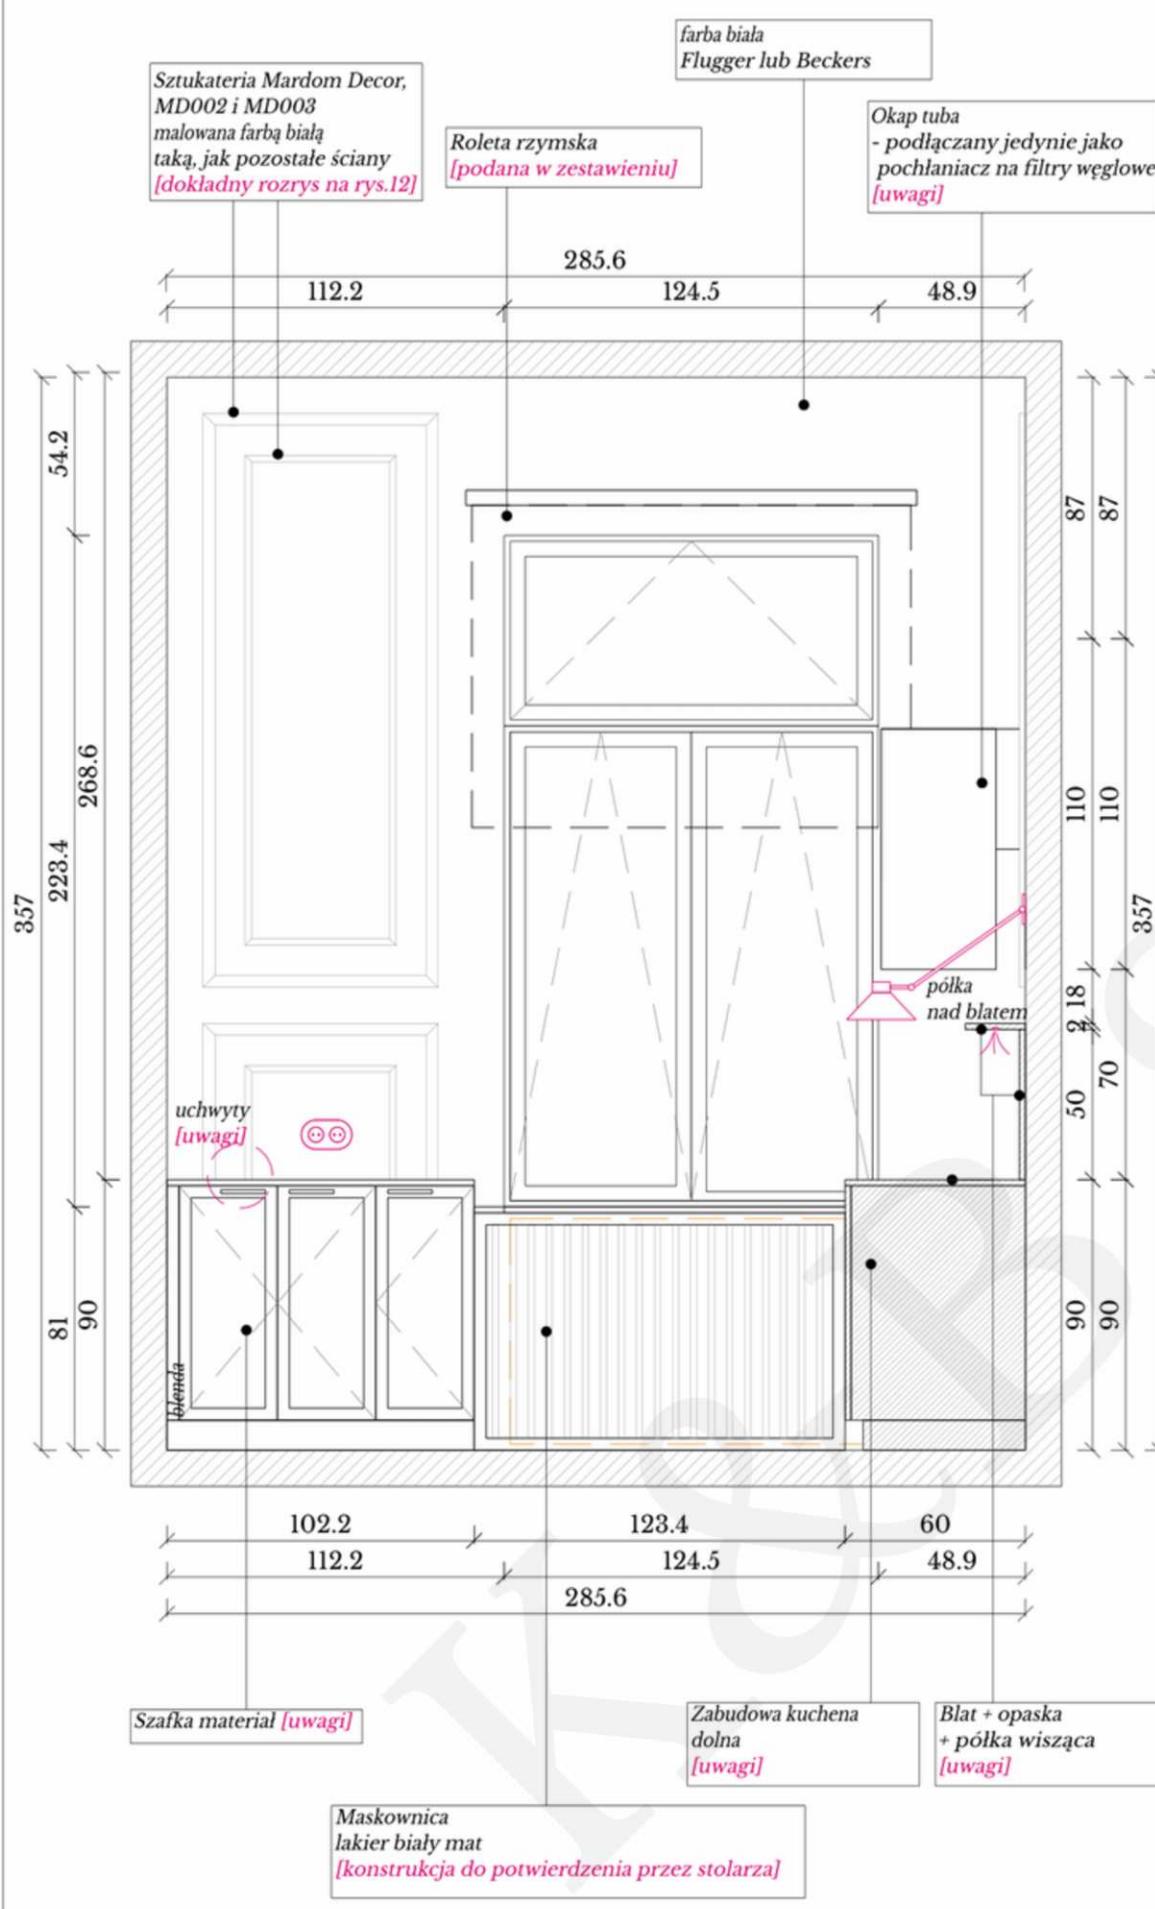

# PRZEKROJE / INSTALACJE ELEKTRYCZNE

## PRZEKRÓJ B-B

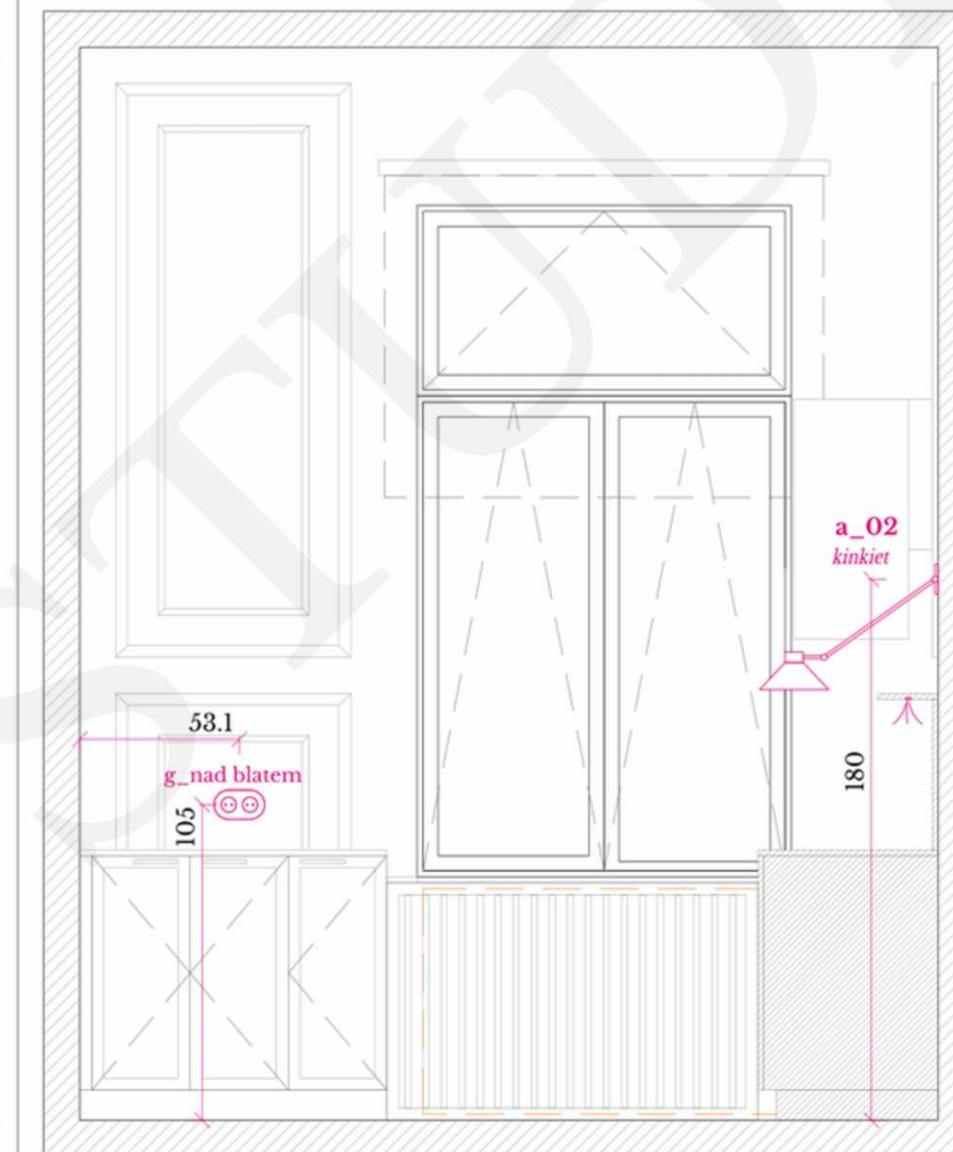


### LEGENDA

	ŚCIANY ISTNIEJĄCE
--	-------------------

### MATERIAŁY [UWAGI]

BLAT + OPASKA NAD BLATEM + PÓŁKA  
konglomerat kwarcowy  
Bronze Coast lub Calacatta Volegno  
gr. 2 cm  
TechniStone

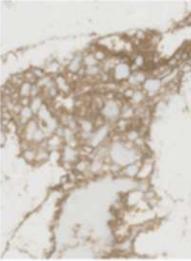

### FRONTY + WNĘTRZE

fronty frezowane - ramka 4 cm  
lakier granatowy mat RAL 5000 lub RAL 5013 lub RAL 5026  
[proszę o przygotowanie próbek frontów do powyższych kolorów]

wnętrze  
płyta laminowana dobrana pod kolor wybranego koloru frontu

SZUFLADY SYSTEM  
antaro BLUM


### UCHWYTY

Uchwyt RELING MOSIĘŻNY  
rozstaw: 128mm  
Hvyt



### GNIAZDA PRĄDOWE I WŁĄCZNIKI

-kolekcja Vectis Round  
-kolor biały  
-rodzaje ramek podane na rzucie obok

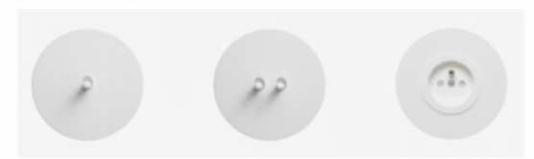

### UWAGI PROJEKTOWE:

- Przed przystąpieniem do prac należy dokładnie przejrzeć wszystkie rysunki i potwierdzić ich zgodność z Architektem i Inwestorem
- Wymiary należy sprawdzić na budowie. W momencie wystąpienia widocznych różnic pomiędzy wymiarami na rysunkach, a w rzeczywistości należy skontaktować się z architektem.


Studio  
projektowania  
wnętrz



NAZWA INWESTYCJI:	PROJEKT KUCHNI Z JADALNIĄ	NUMER RYSUNKU: 09
ADRES INWESTYCJI:		SKALA RYSUNKU: 1:25
INWESTOR:	KUCHNIA PRZEKRÓJE B-B ARANŻACJA ELEKTRYKA	DATA OPRACOWANIA: 26.02.2024r.
ARCHITEKT:	MGR INŻ. ARCH. KAROLINA RUSINEK TEL.: 696 850 891	PODPIS:

# PRZEKROJE / ARANŻACJA / INSTALACJE ELEKTRYCZNE

## PRZEKRÓJ C-C

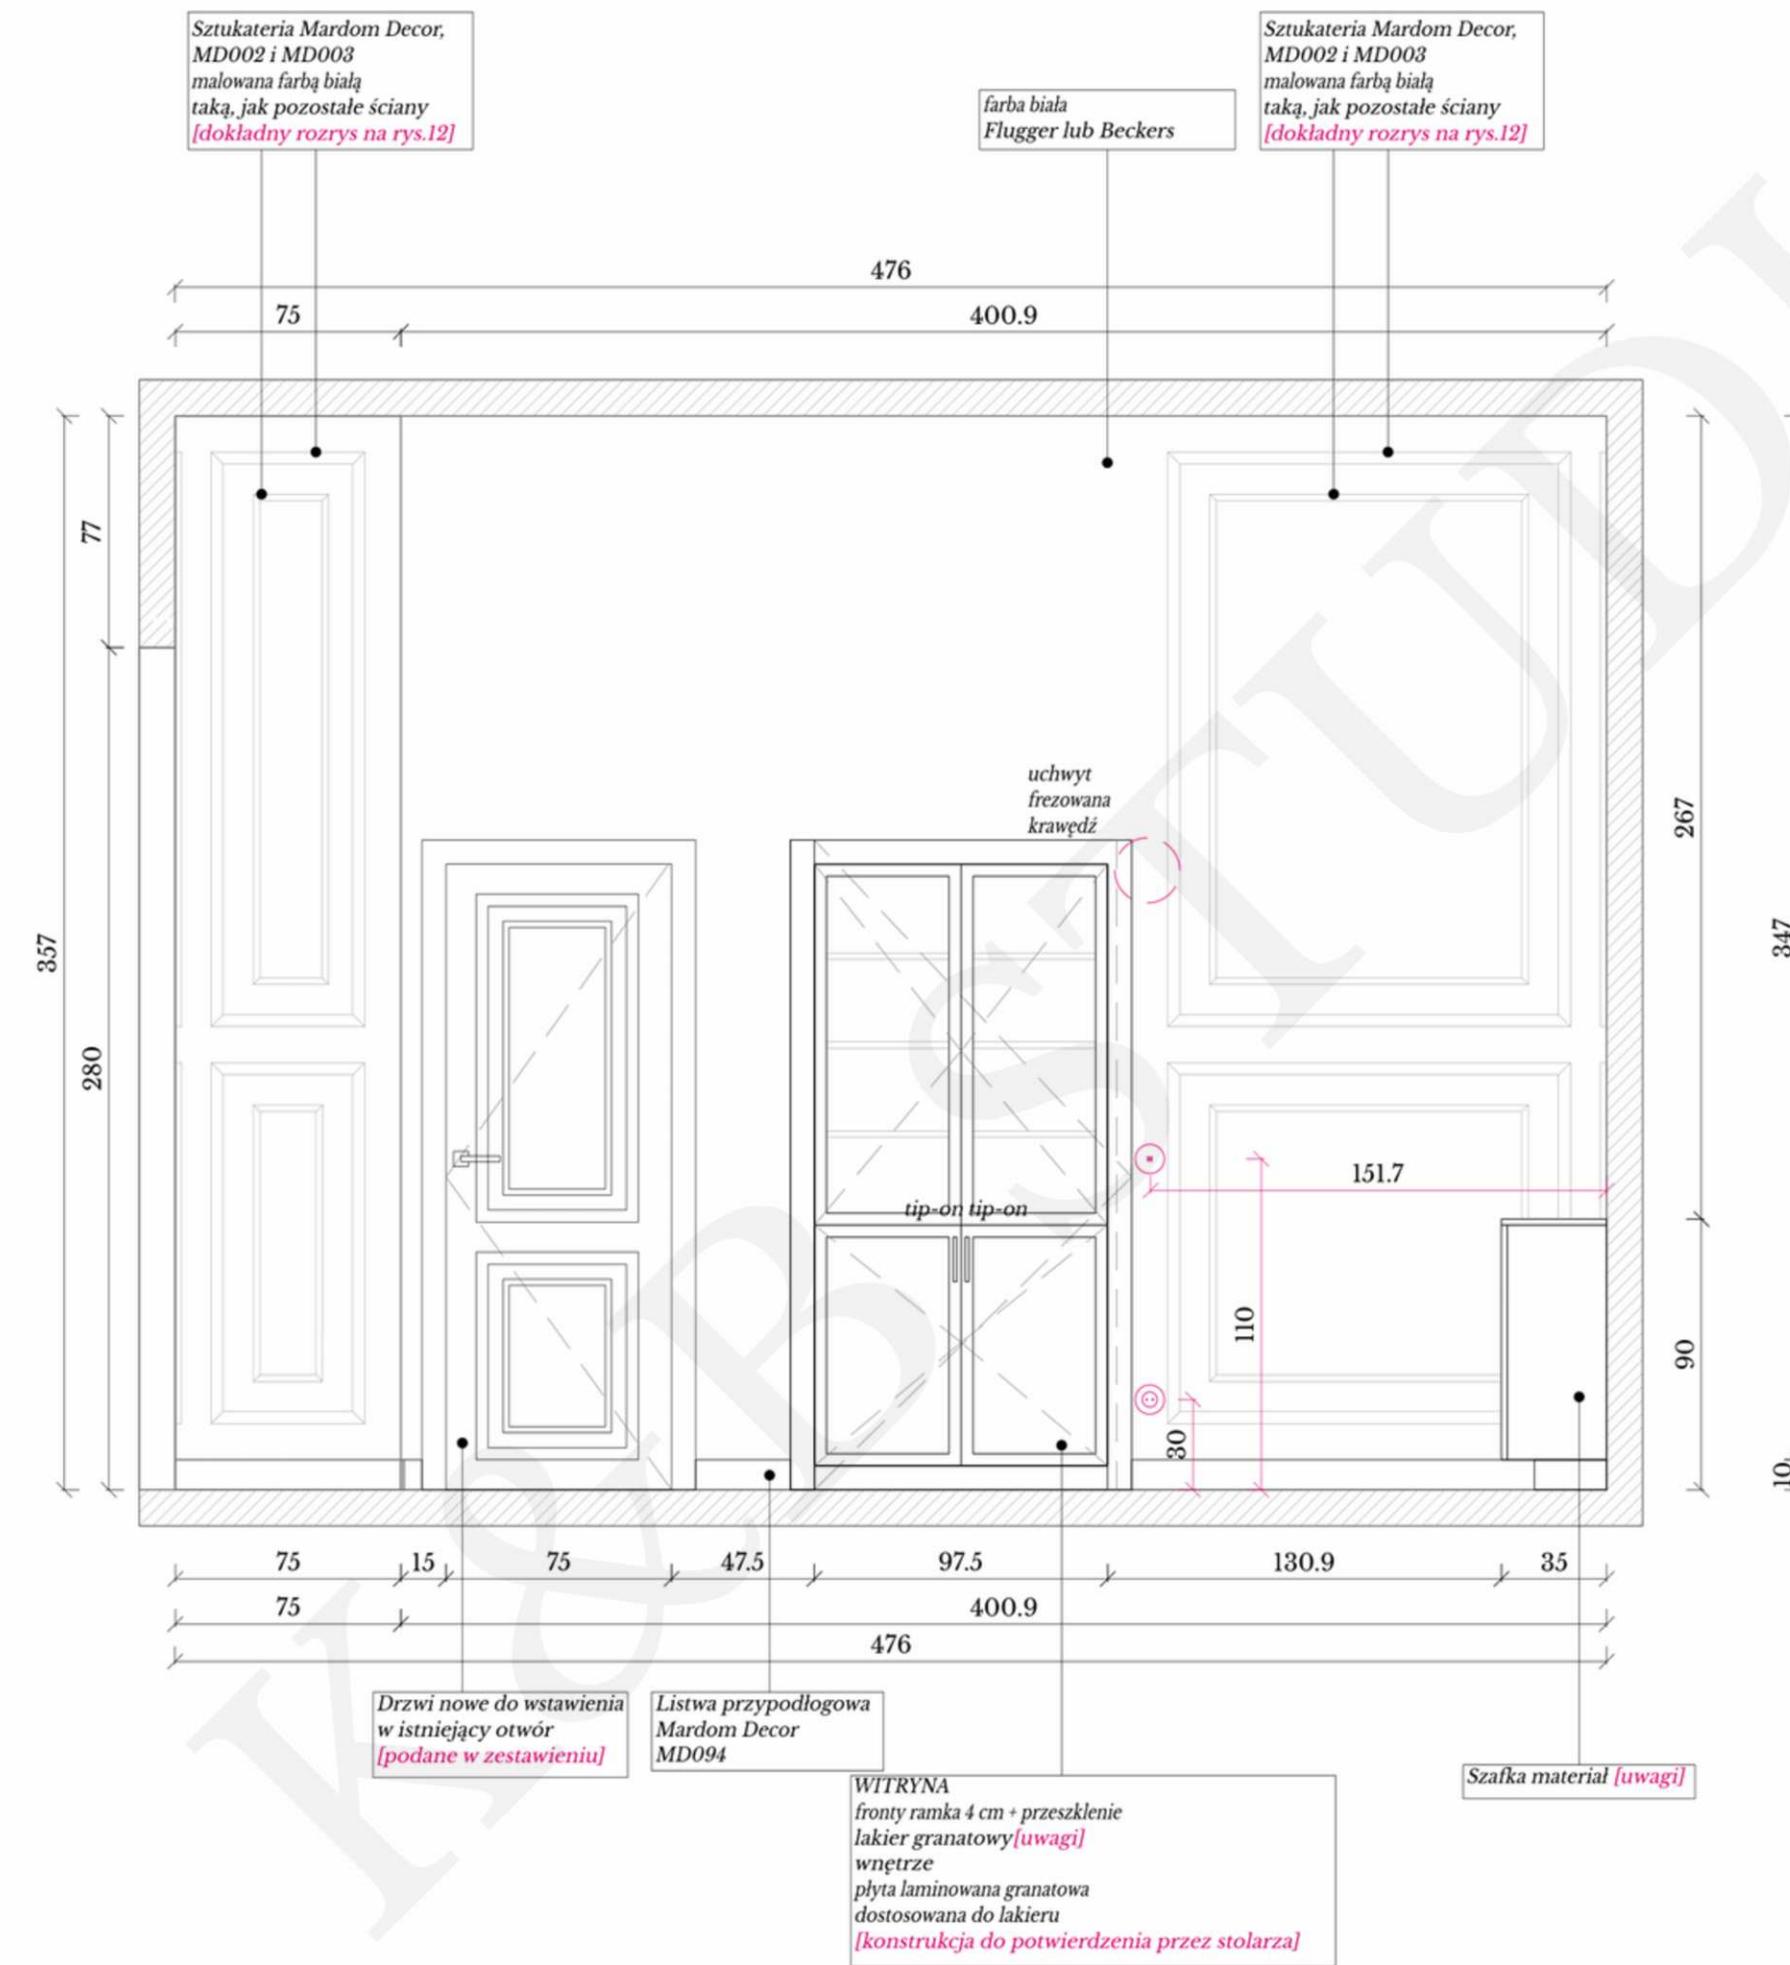


## LEGENDA



ŚCIANY ISTNIEJĄCE

## MATERIAŁY [UWAGI]

BLAT + OPASKA NAD BLATEM + PÓŁKA  
konglomerat kwarcowy  
Bronze Coast lub Calacatta Volegno  
gr. 2 cm  
TechniStone

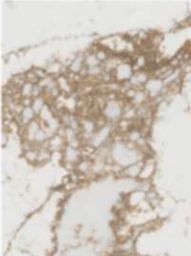

## FRONTY + WNĘTRZE

fronty frezowane - ramka 4 cm  
lakier granatowy mat RAL 5000 lub RAL 5013 lub RAL 5026  
[proszę o przygotowanie próbek frontów do powyższych kolorów]

wnętrze  
plyta laminowana dobrana pod kolor wybranego koloru frontu

SZUFLADY SYSTEM  
antaro BLUM

## UCHWYTY

Uchwyt RELING MOSIĘŻNY  
rozstaw: 128mm  
Hvyt



## GNIAZDA PRĄDOWE I WŁĄCZNIKI

kolekcja Vectis Round  
kolor biały  
rodzaje ramek podane na rzucie obok



## UWAGI PROJEKTOWE:

- Przed przystąpieniem do prac należy dokładnie przejrzeć wszystkie rysunki i potwierdzić ich zgodność z Architektem i Inwestorem
- Wymiary należy sprawdzić na budowie. W momencie wystąpienia widocznych różnic pomiędzy wymiarami na rysunkach, a w rzeczywistości należy skontaktować się z architektem.


Studio  
projektowania  
wnętrz



NAZWA INWESTYCJI:	PROJEKT KUCHNI Z JADALNIĄ	NUMER RYSUNKU: 10
ADRES INWESTYCJI:		SKALA RYSUNKU: 1:25
INWESTOR:	KUCHNIA PRZEKROJE C-C ARANŻACJA ELEKTRYKA	DATA OPRACOWANIA: 26.02.2024r.
ARCHITEKT: MGR INŻ. ARCH. KAROLINA RUSINEK TEL.: 696 850 891	PODPIS:	

# PRZEKROJE / ARANŻACJA

## PRZEKRÓJ D-D

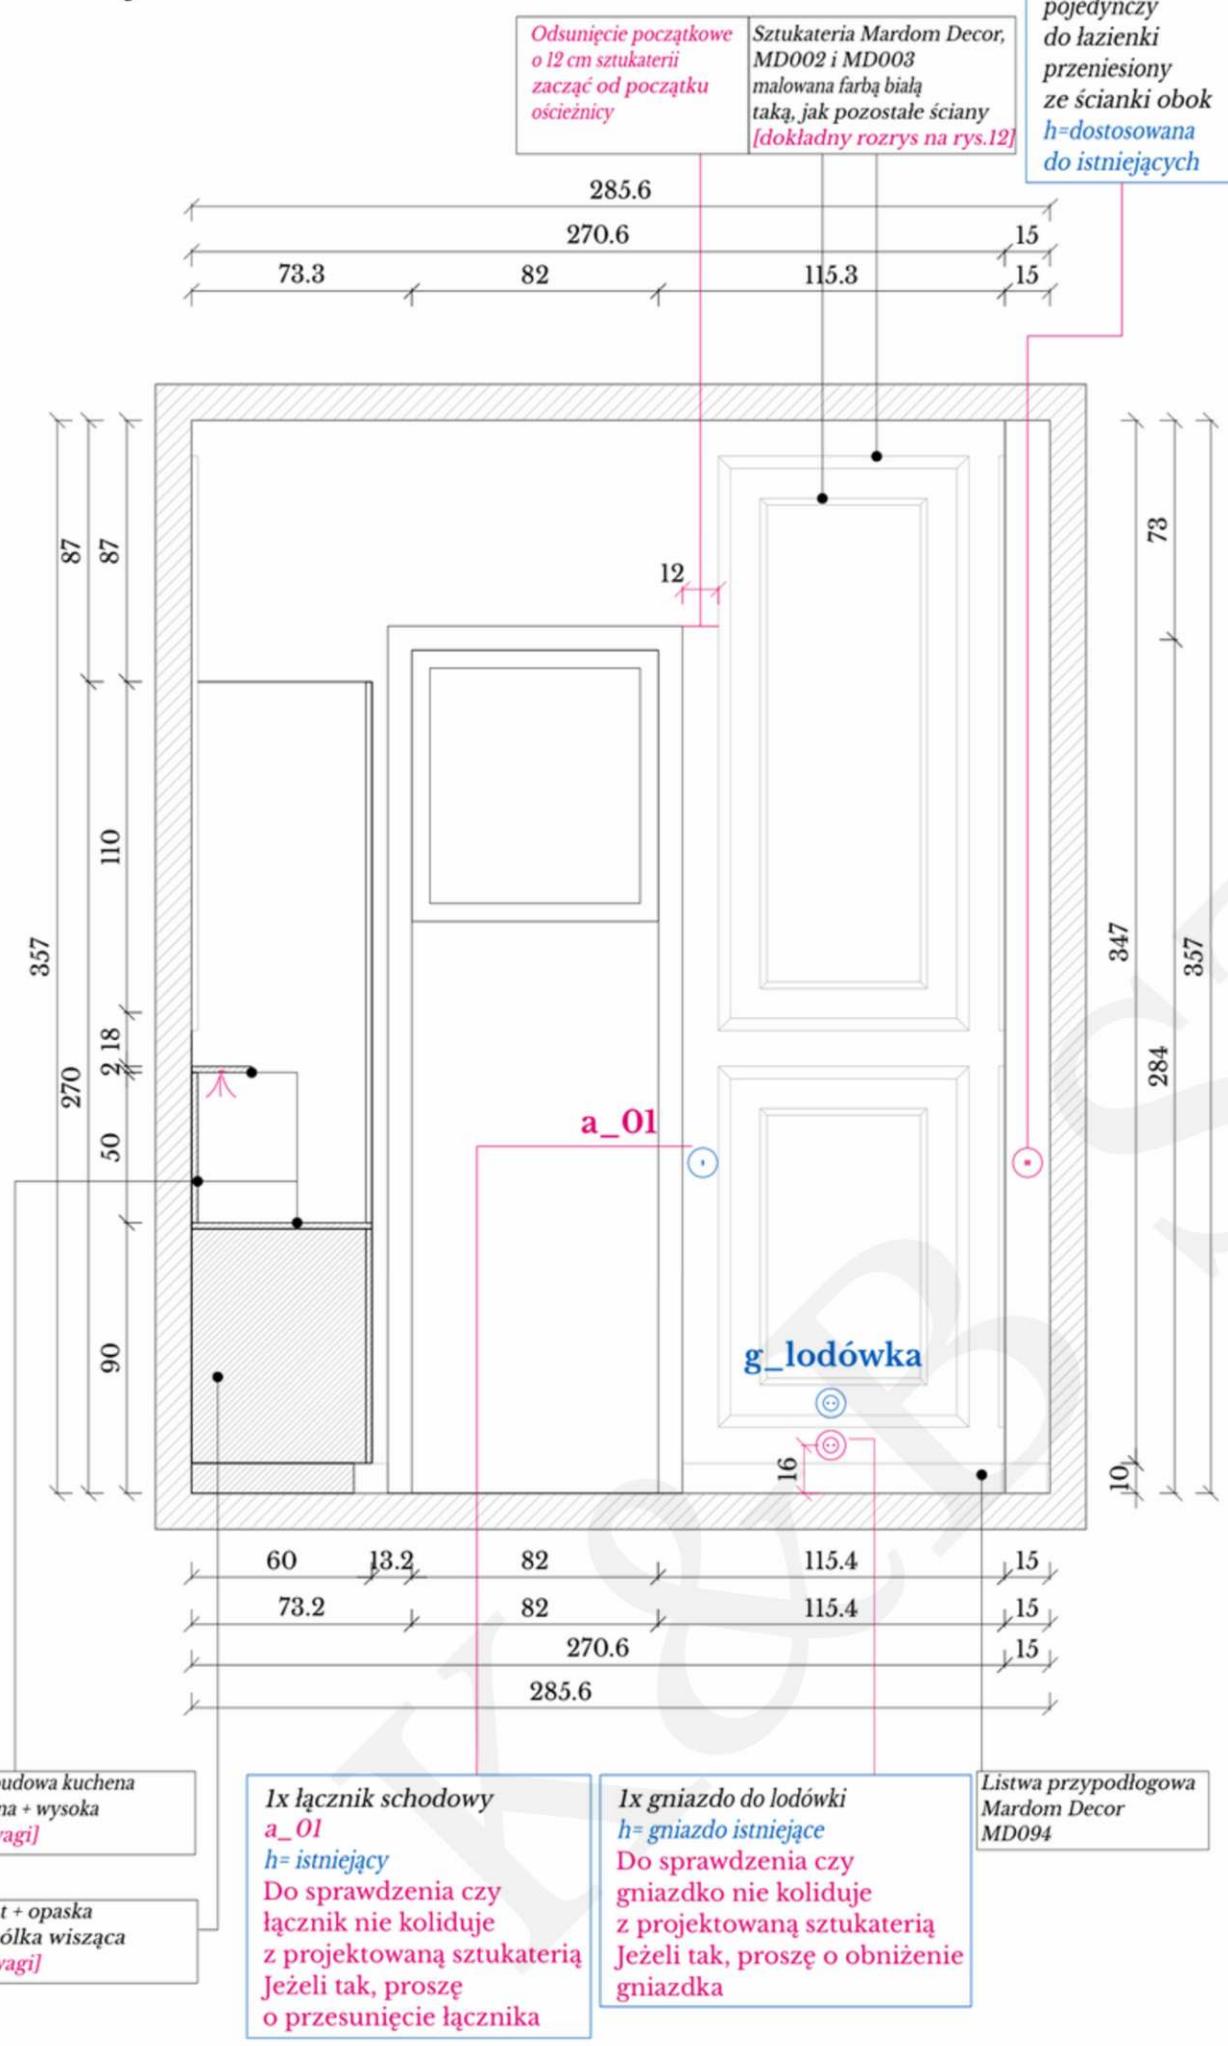


# BLAT + OPASKA + PÓŁKA

## ROZRYS ELEMENTÓW


materiał : konglomerat kwarcowy  
Bronze Coast lub Calacatta Volegno  
TechniStone

**Wycena: proszę o wycenę blatów, półki i opaski w grubości 2 cm**

**BLAT I**  
**OPASKA NAD BLATEM**  
**PÓŁKA NAD BLATEM + LED**

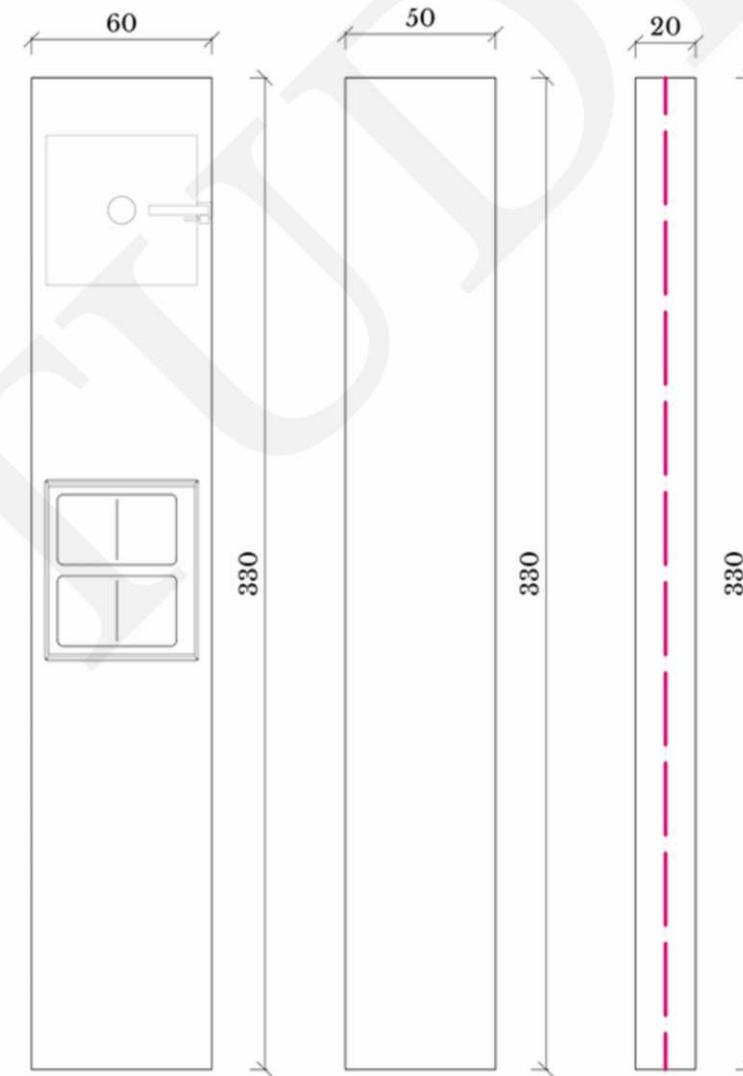

## BLAT II

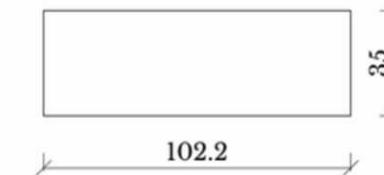

## LEGENDA

	ŚCIANY ISTNIEJĄCE
--	-------------------

## FRONTY + WNĘTRZE

fronty frezowane - ramka 4 cm  
lakier granatowy mat RAL 5000 lub RAL 5013 lub RAL 5026  
[proszę o przygotowanie próbek frontów do powyższych kolorów]

wnętrze  
płyta laminowana dobrana pod kolor wybranego koloru frontu

## SZUFLADY SYSTEM

antaro BLUM

## UCHWYTY

Uchwyt RELING MOSIĘŻNY  
rozstaw: 128mm  
Hvyt



## GNIAZDA PRĄDOWE I WŁĄCZNIKI

-kolekcja Vectis Round  
-kolor biały  
-rodzaje ramek podane na rzucie obok



## UWAGI PROJEKTOWE:

- Przed przystąpieniem do prac należy dokładnie przejrzeć wszystkie rysunki i potwierdzić ich zgodność z Architektem i Inwestorem
- Wymiary należy sprawdzić na budowie. W momencie wystąpienia widocznych różnic pomiędzy wymiarami na rysunkach, a w rzeczywistości należy skontaktować się z architektem.


Studio projektowania wnętrz



NAZWA INWESTYCJI:	PROJEKT KUCHNI Z JADALNIĄ	NUMER RYSUNKU:
ADRES INWESTYCJI:		SKALA RYSUNKU:
INWESTOR:		1:25
KUCHNIA PRZEKROJE B-B ARANŻACJA ELEKTRYKA		DATA OPRACOWANIA:
ARCHITEKT: MGR INŻ. ARCH. KAROLINA RUSINEK TEL.: 696 850 891		26.02.2024r.
		PODPIS:

# SZTUKATERIA NA ŚCIANACH, OKAP ZABUDOWANY - ROZRYS

WIDOK A-A

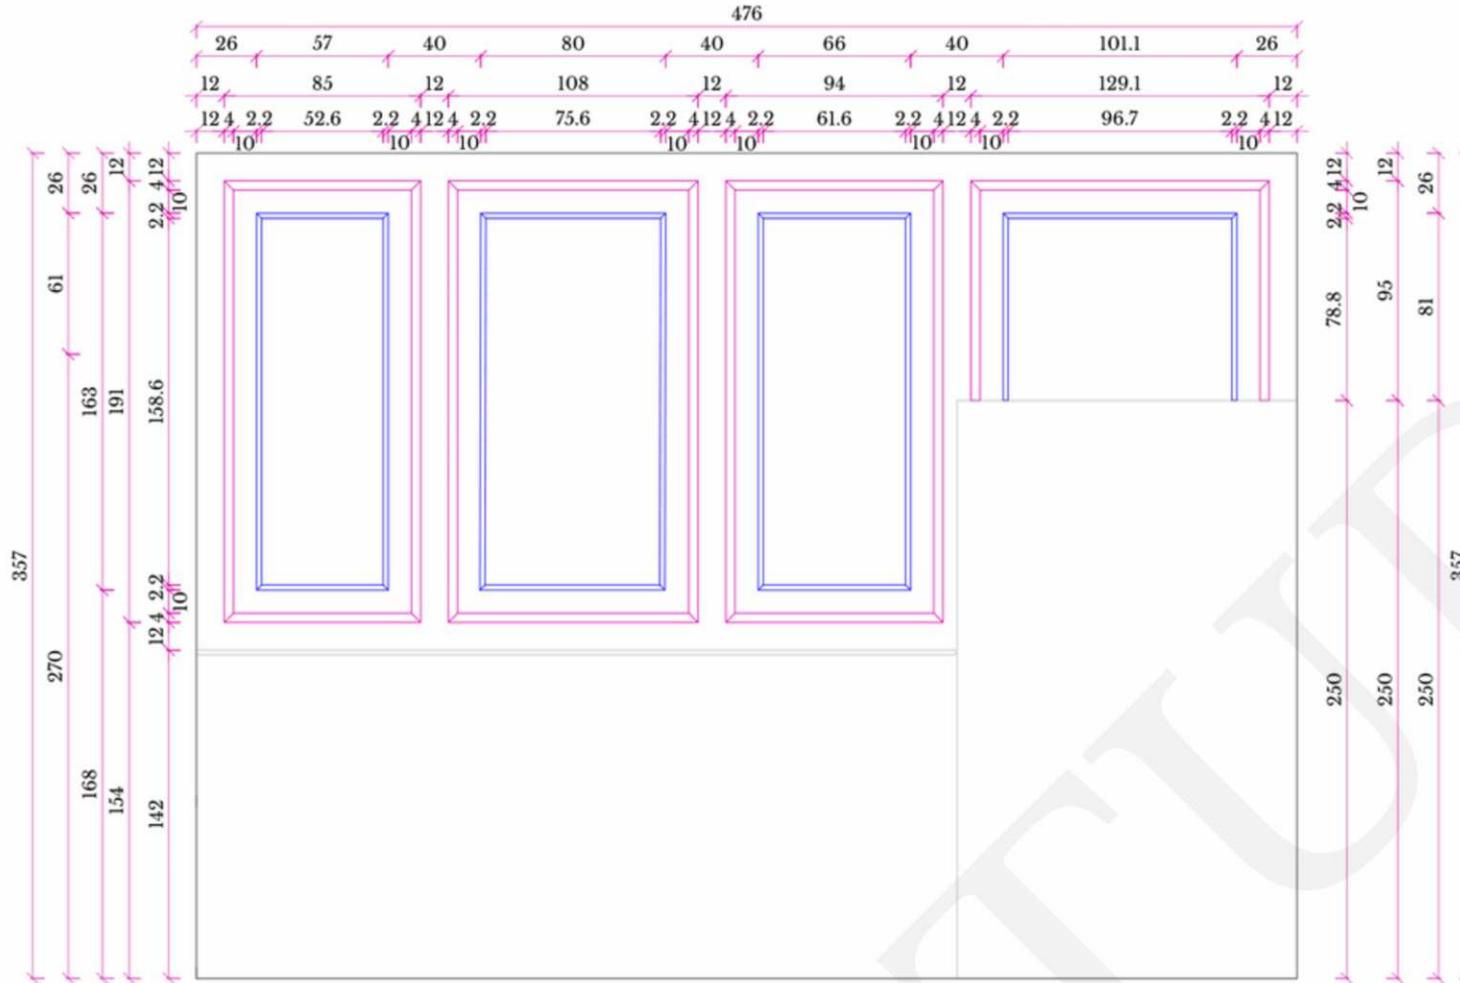

## LEGENDA

### MATERIAŁY [UWAGI]


**sztukateria ścenna**  
MD003 z polimeru HD  
2.2 x 1 x 200 cm  
[Mardom Decor]




**sztukateria ścenna**  
MD002 z polimeru HD  
4 x 1.8 x 200 cm  
[Mardom Decor]




ŚCIANY ZA SZAFKĄ I STOŁEM  
WIDOK B-B

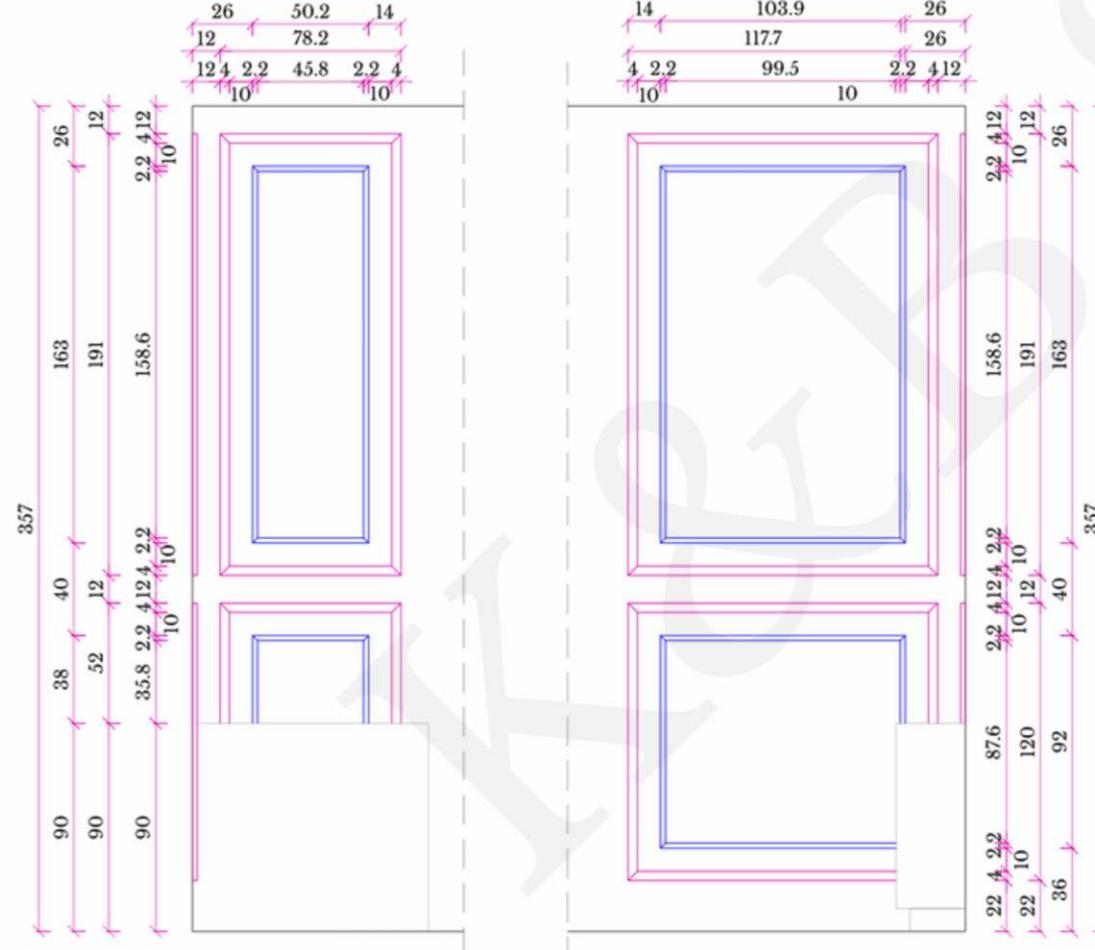


WIDOK C-C

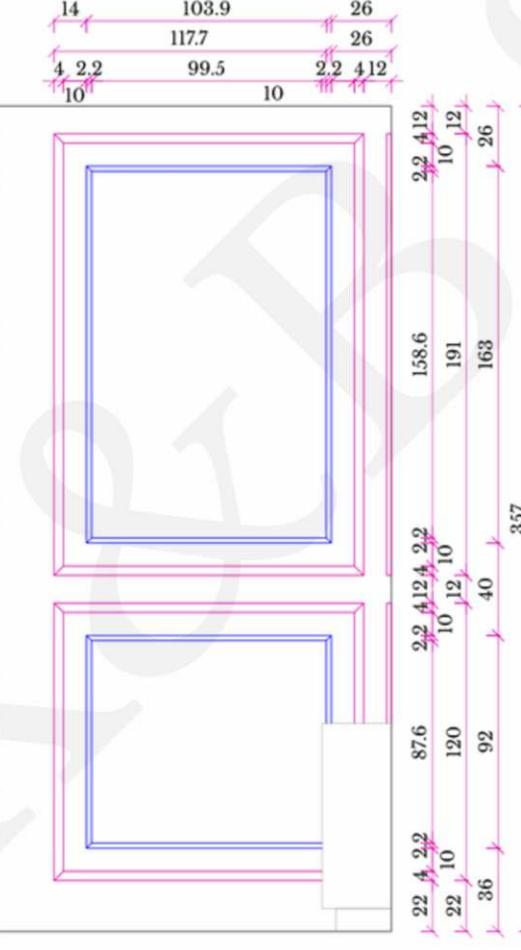

ŚCIANY ZA LODÓWKĄ  
WIDOK C-C

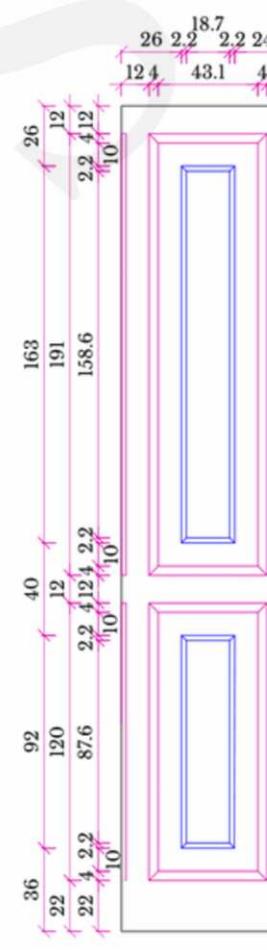

WIDOK D-D

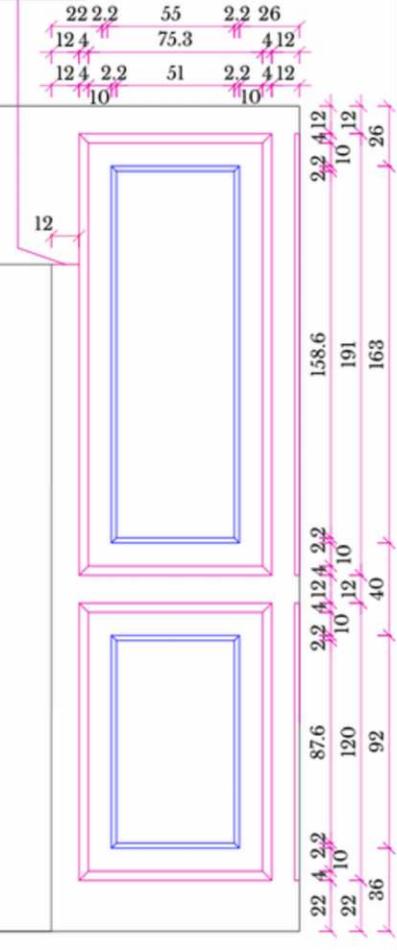

Odsunięcie początkowe  
o 12 cm sztukaterii  
zacząć od początku  
osiecznicy

**UWAGI PROJEKTOWE:**  
1. Przed przystąpieniem do prac należy dokładnie przejrzeć wszystkie rysunki i potwierdzić ich zgodność z Architektem i Inwestorem  
2. Wymiary należy sprawdzić na budowie. W momencie wystąpienia widocznych różnic pomiędzy wymiarami na rysunkach, a w rzeczywistości należy skontaktować się z architektem.

Studio  
projektowania  
wnętrz




NAZWA INWESTYCJI:	PROJEKT KUCHNI Z JADALNIĄ	NUMER RYSUNKU:
ADRES INWESTYCJI:		SKALA RYSUNKU:
INWESTOR:		-
SZTUKATERIA OKAP ZABUDOWANY ROZRYSY		DATA OPRACOWANIA:
	26.02.2024r.	PODPIS:
ARCHITEKT:	MGR INŻ. ARCH. KAROLINA PLECH TEL.: 696 850 891	


# RYSUNKI DLA STOLARZA RYS. 1

## ZABUDOWA KUCHENNA


### FRONT

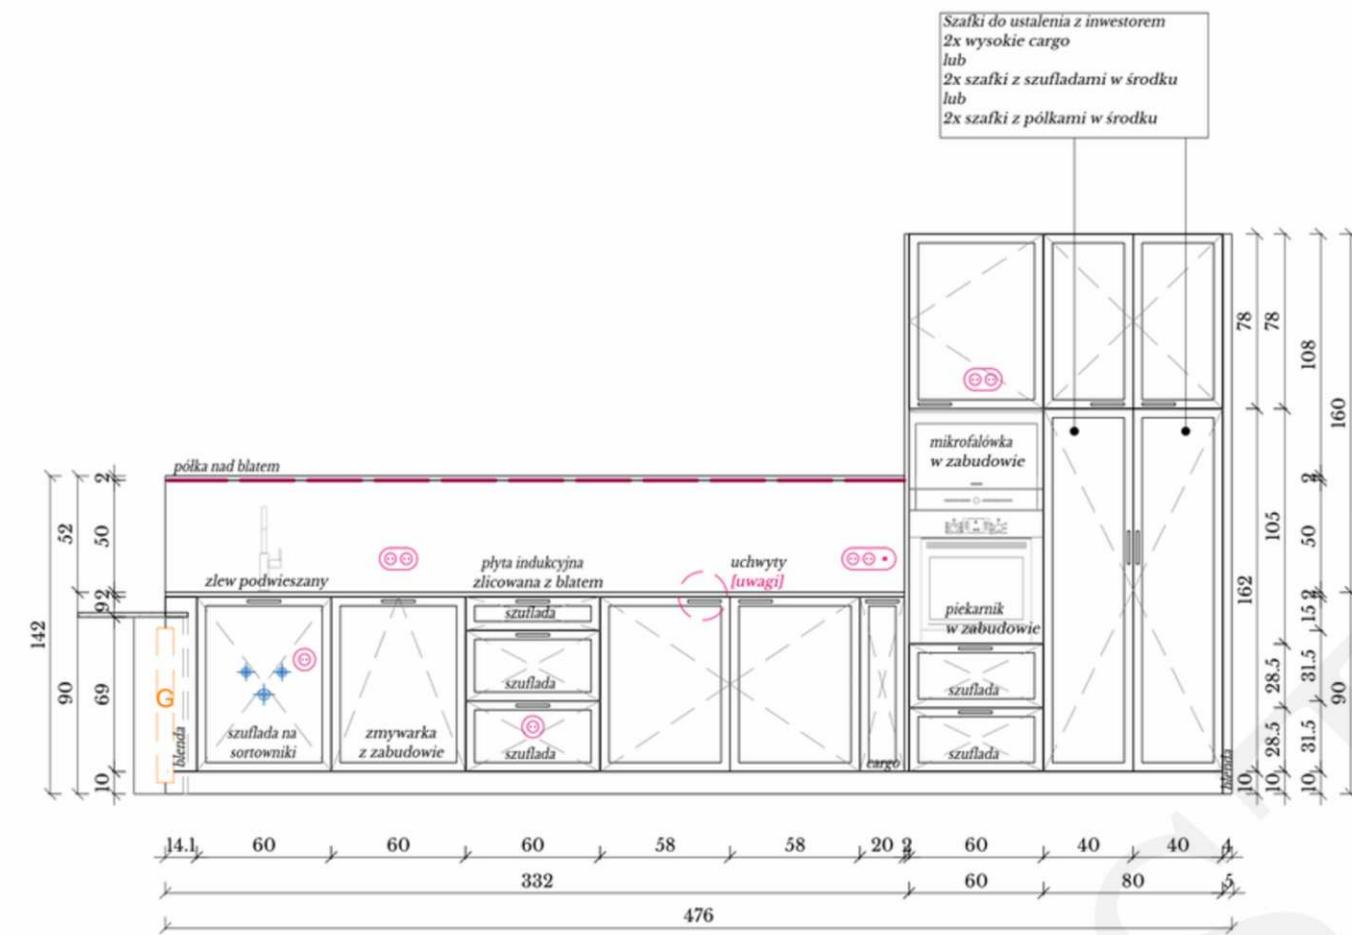

### WNĘTRZE

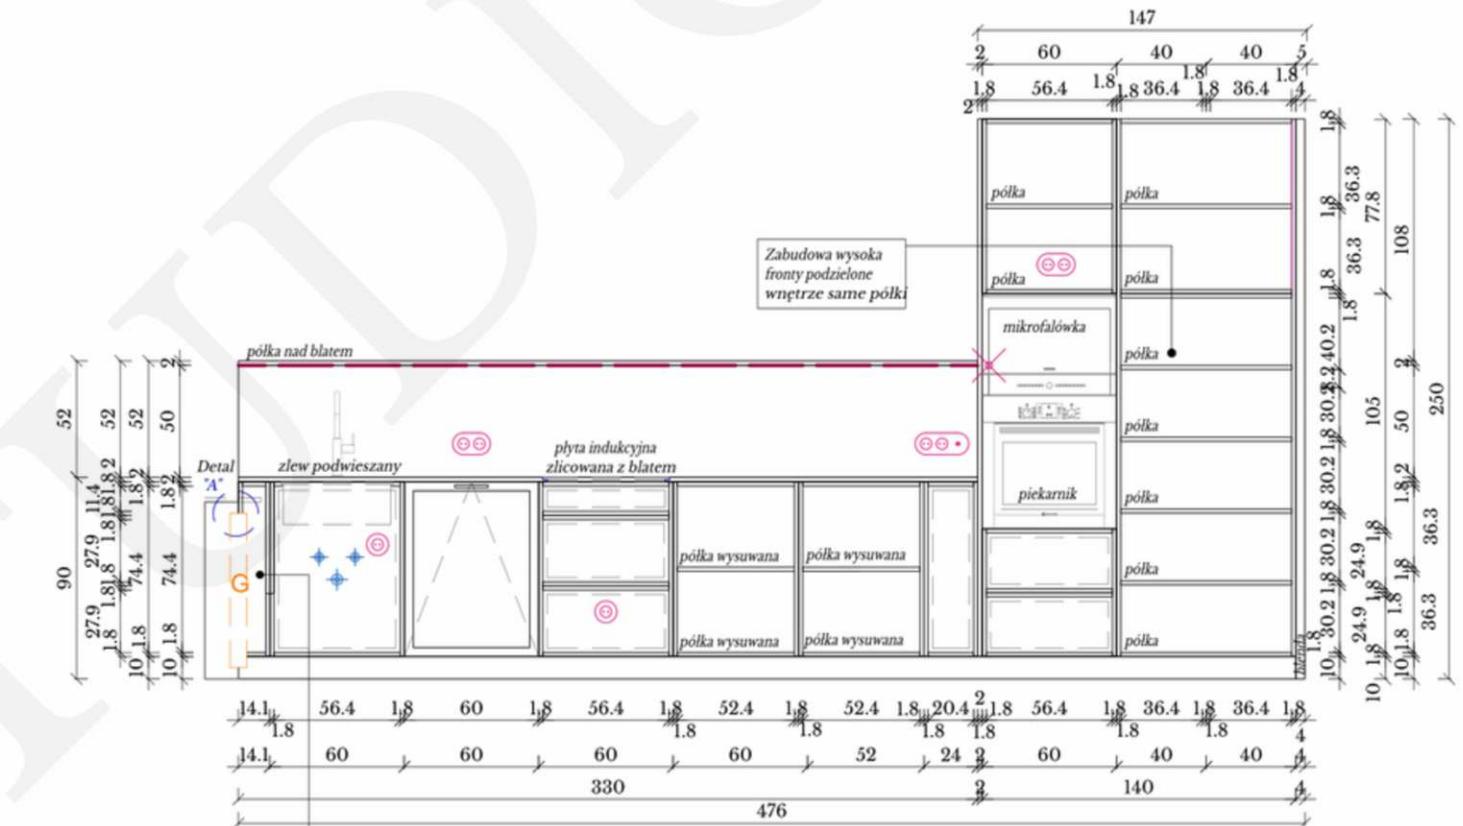


### RZUT

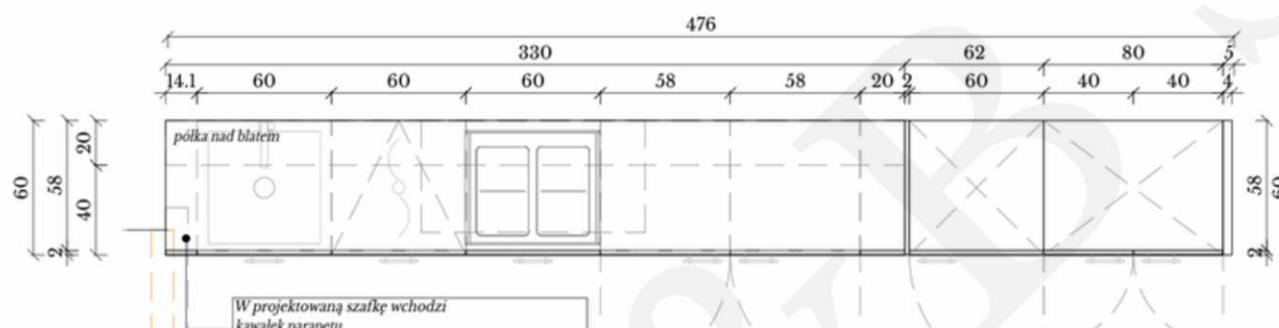

### UWAGI

#### MATERIAŁY

BLAT + OPASKA NAD BLATEM + PÓŁKA  
konglomerat kwarcowy  
Bronze Coast lub Calacatta Volegno  
gr. 2 cm  
TechniStone

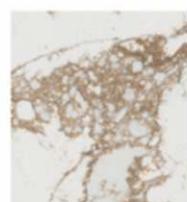

#### FRONTY + WNĘTRZE

fronty frezowane - ramka 4 cm  
lakier granatowy mat RAL 5000 lub RAL 5013 lub RAL 5010  
[proszę o przygotowanie próbek frontów do powyższych wnętrze]  
płyta laminowana dobrana pod kolor wybranego koloru frontu

#### Detal A'




#### SZUFLADY SYSTEM




RYSUNKI DLA STOLARZA RYS. 2

WITRYNA RUCHOMA


FRONT

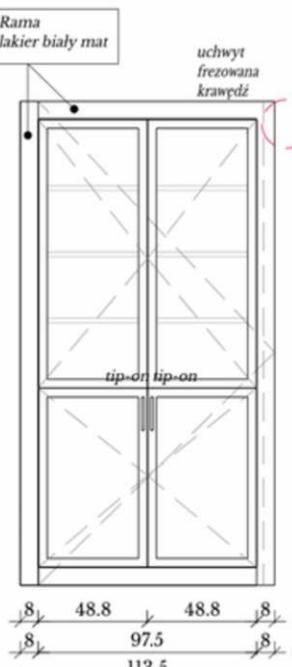


WNETRZE

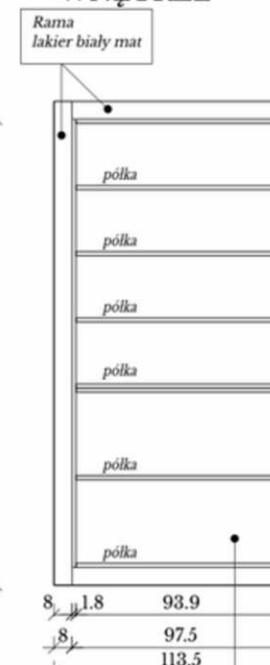

PRZEKRÓ

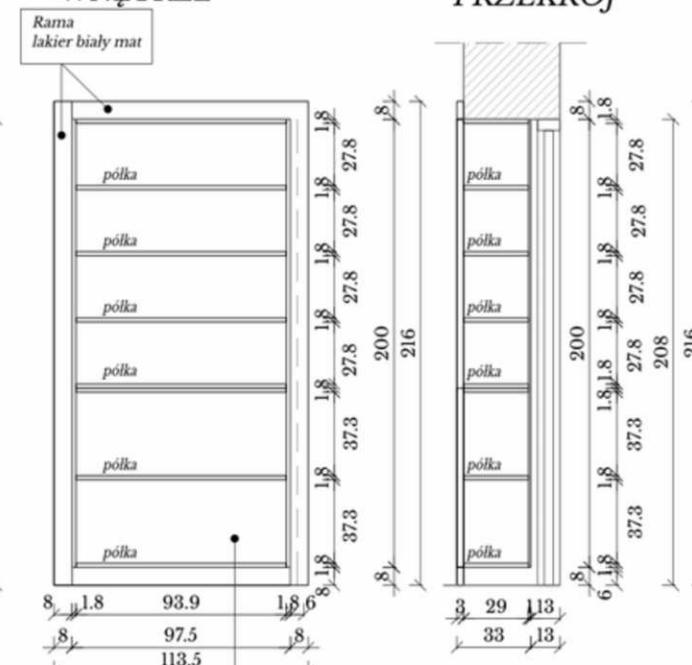


RZUT

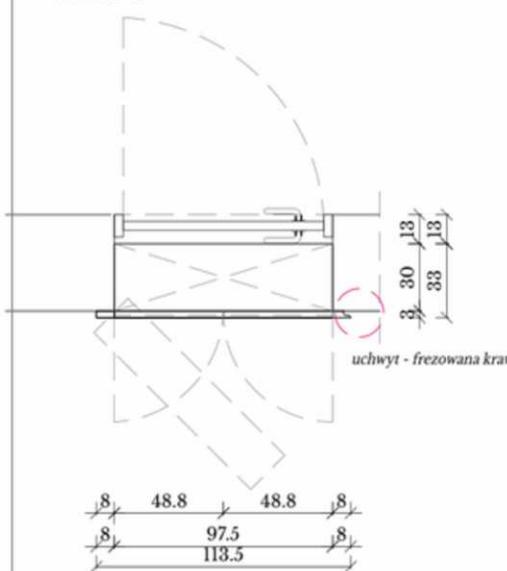


**WITRYNA**  
fronty ramka 4 cm + przeszkleńie  
lakier granatowy [uwagi]  
wnętrze  
piły laminowana granatowa  
dososowana do lakieru  
[konstrukcja do potwierdzenia przez stolarza]

*SZAFKI + MASKOWNICA ZAKRYWAJĄCA GRZEJNIK]*


FRONT

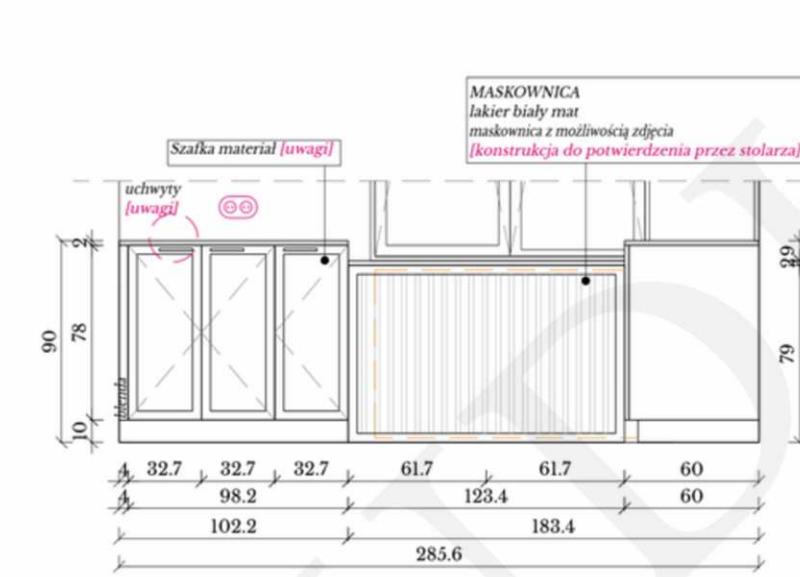

WNETRZE

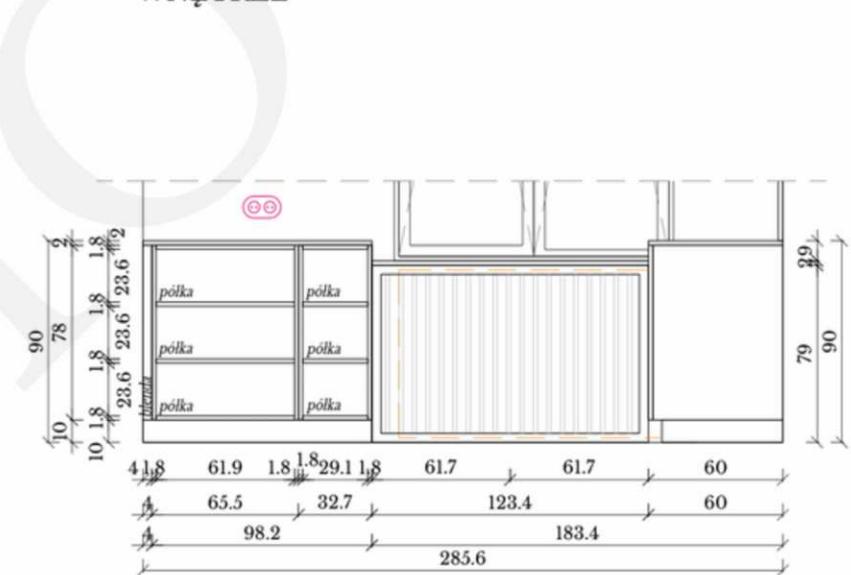

RZU

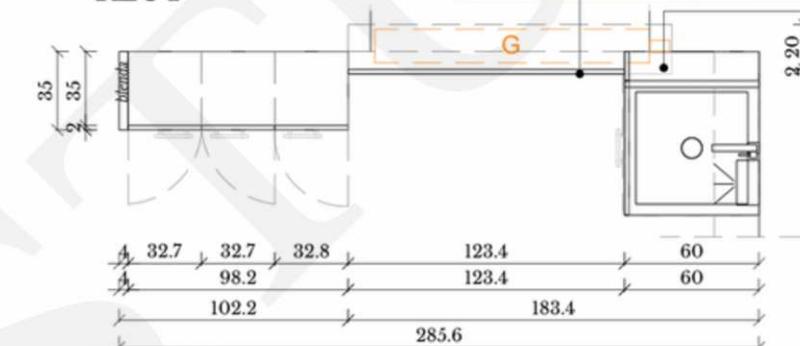


**DOSTĘP DO GRZALKI**  
dostęp do grzalki od środka w szafce z szufladą  
na sortowniki pod złewem  
*[konstrukcja do potwierdzenia przez stolarza]*

UWAGI

MATERIAŁY

**BLAT + OPASKA NAD BLATEM + PÓŁKA**  
konglomerat kwarcowy  
*Bronze Coast lub Calacatta Volegno*  
gr. 2 cm  
TechniStone

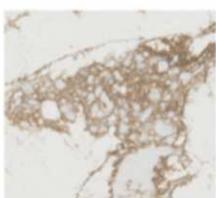

FRONTY + WNETRZE

fronty frezowane - ramka 4 cm  
lakier granatowy mat RAL 5000 lub RAL 5013 lub RAL 5026  
[proszę o przygotowanie próbek frontów do powyższych kolorów]  
wnętrze  
płyta laminowana dobrana pod kolor wybranego koloru frontu

SZUFLADY SYSTEM  
antaro BLUM

UCHWYTY

**UCHWYT RELING MOSIĘŻNY  
rozstaw: 128mm  
Hvyt**



K  
B

K & B STUDIO  
projektowanie  
wnętrz



K  
B

K & B STUDIO  
projektowanie  
wnętrz



K  
B

K & B STUDIO  
projektowanie  
wnętrz





K & B STUDIO  
projektowanie  
wnętrz

