


ZESTAWIENIE POWIERZCHNI		
NR	NAZWA POMIESZCZENIA	POW. [M ²]
0.01	ŁAZIENKA	4,57
LEGENDA		
	ŚCIANY ISTNIEJĄCE	
	WENTYLACJA [KRATKA] ISTNIEJĄCA LUB PROJEKTOWANA	
	GRZEJNIK PROJEKTOWANY	
	PIEC GAZOWY	
	ŁĄCZNIK POJEDYNCZY	INSTALACJE ELEKTRYCZNE ISTNIEJĄCE
	ŁĄCZNIK PODWÓJNY	OŚWIETLENIE NATYNKOWE
	ŁĄCZNIK SZEREGOWY	OŚWIETLENIE WPUSZCZANE
	ŁĄCZNIK KRZYŻOWY	LAMPA WISZĄCA
	ŁĄCZNIK SCHODOWY POJEDYNCZY	KINKIET
	ŁĄCZNIK SCHODOWY PODWÓJNY	WYPUST DO LED
	GNIAZDO POJEDYNCZE W JEDNEJ PUSZCE	LED
	GNIAZDO PODWÓJNE W JEDNEJ PUSZCE	

RZUT PODSTAWOWY / INSTALACJE ELEKTRYCZNE

2x gniazdo podwójne umieszczone w szafce nad WC [wszystko w jednej ramce] h=135 cm

1x gniazdo pojedyncze do pralki
h=90 cm

1x gniazdo pojedyncze do suszarki
h=205 cm

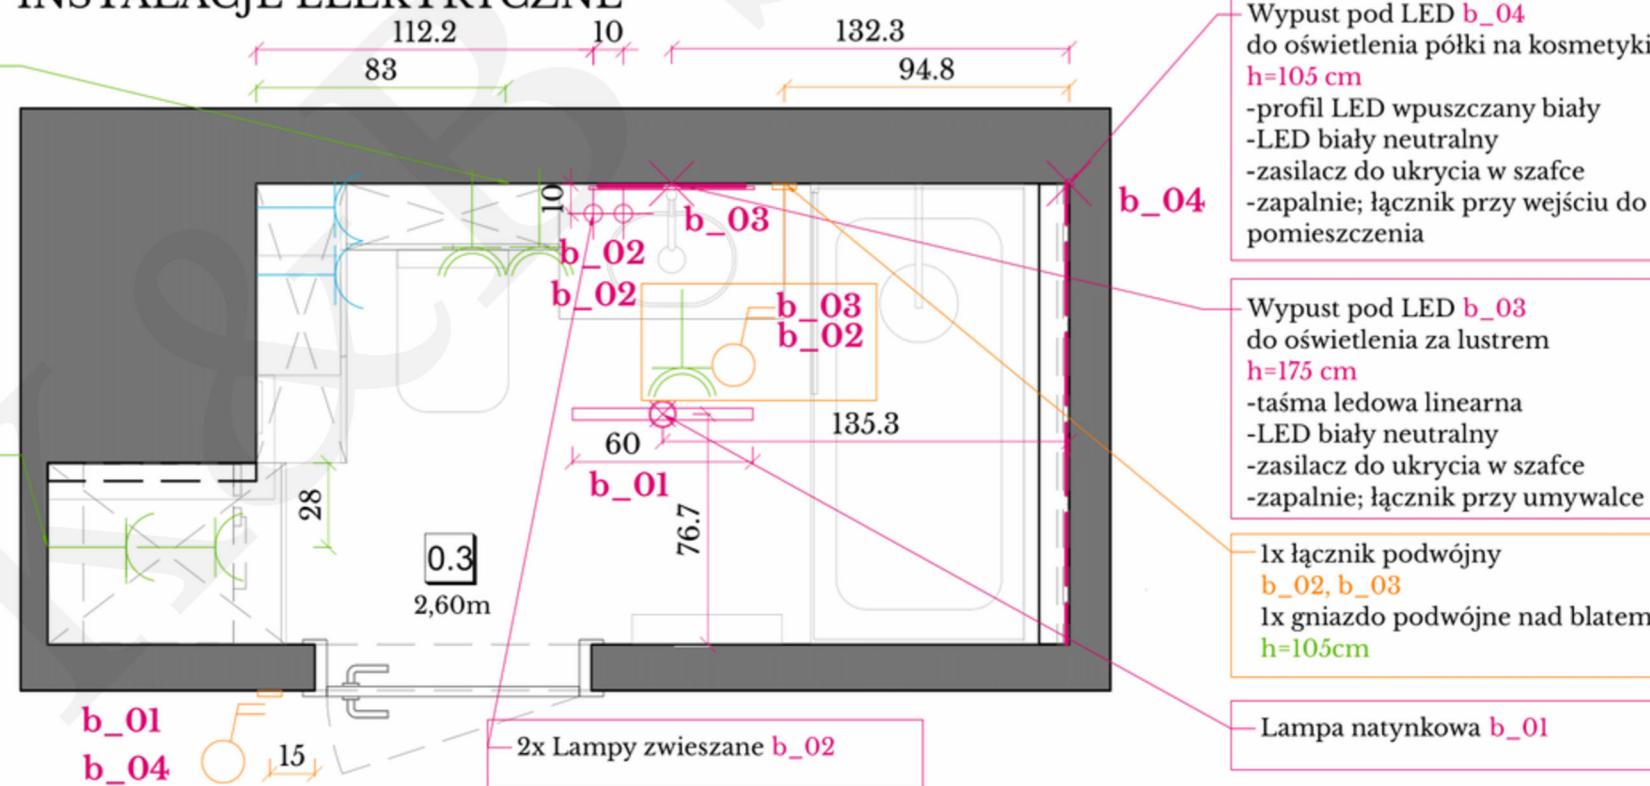

UWAGI PROJEKTOWE:


1. Przed przystąpieniem do prac należy dokładnie przejrzeć wszystkie rysunki i potwierdzić ich zgodność z Architektem i Inwestorem
2. Wymiary należy sprawdzić na budowie. W momencie wystąpienia widocznych różnic pomiędzy wymiarami na rysunkach, a w rzeczywistości należy skontaktować się z architektem.

Studio
projektowania
wnetrz




NAZWA INWESTYCJI:	PROJEKT WNĘTRZA MIESZKANIA	NUMER RYSUNKU: 1A
ADRES INWESTYCJI:		SKALA RYSUNKU: 1:25
INWESTOR:		LAZIENKA RZUTY PODSTAW. ARANŻACJA WOD KAN ELEKTRYKA
ARCHITEKT:	MGR INŻ. ARCH. KAROLINA PLECH TEL.: +48 696 850 891	DATA OPRACOWANIA: lipiec 2024r.

RZUT PODSTAWOWY / UKŁAD PŁYTEK

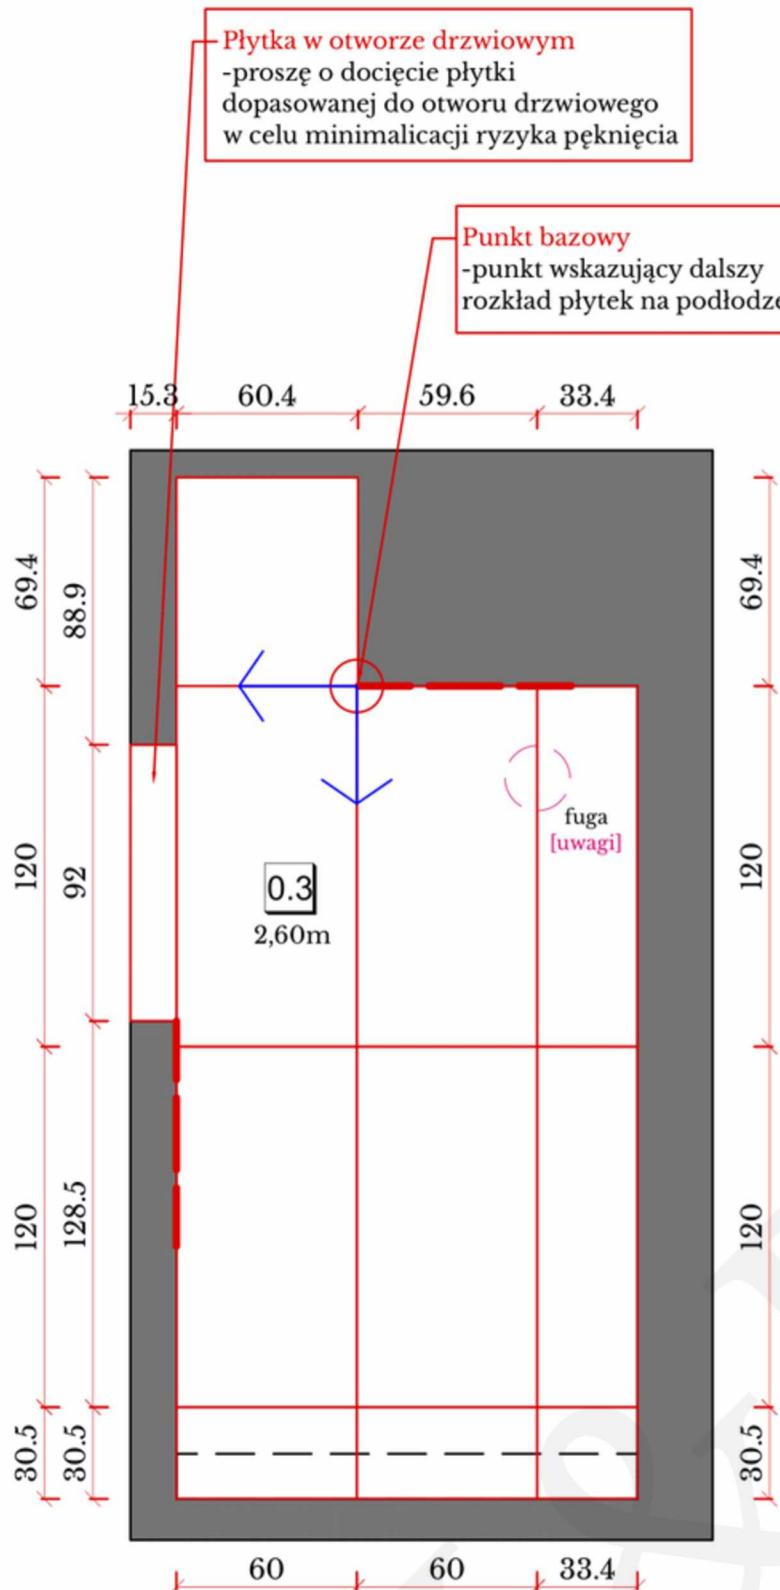

	PŁYTKA PODŁOGOWA 60X120 CM [UWAGI]	Potrzebna ilość: 4,71 m ² + 10% zapasu [ok. 7 szt. + 10% zapasu]
	LISTWA PRZYPODŁOGOWA MD013 Mardom Decor wys. 10 cm	Potrzebna ilość: 1,47 mb + 10% zapasu

RZUT PODSTAWOWY / SUCHA ZABUDOWA / WYBURZENIA / ELEMENTY ŚCIENNE

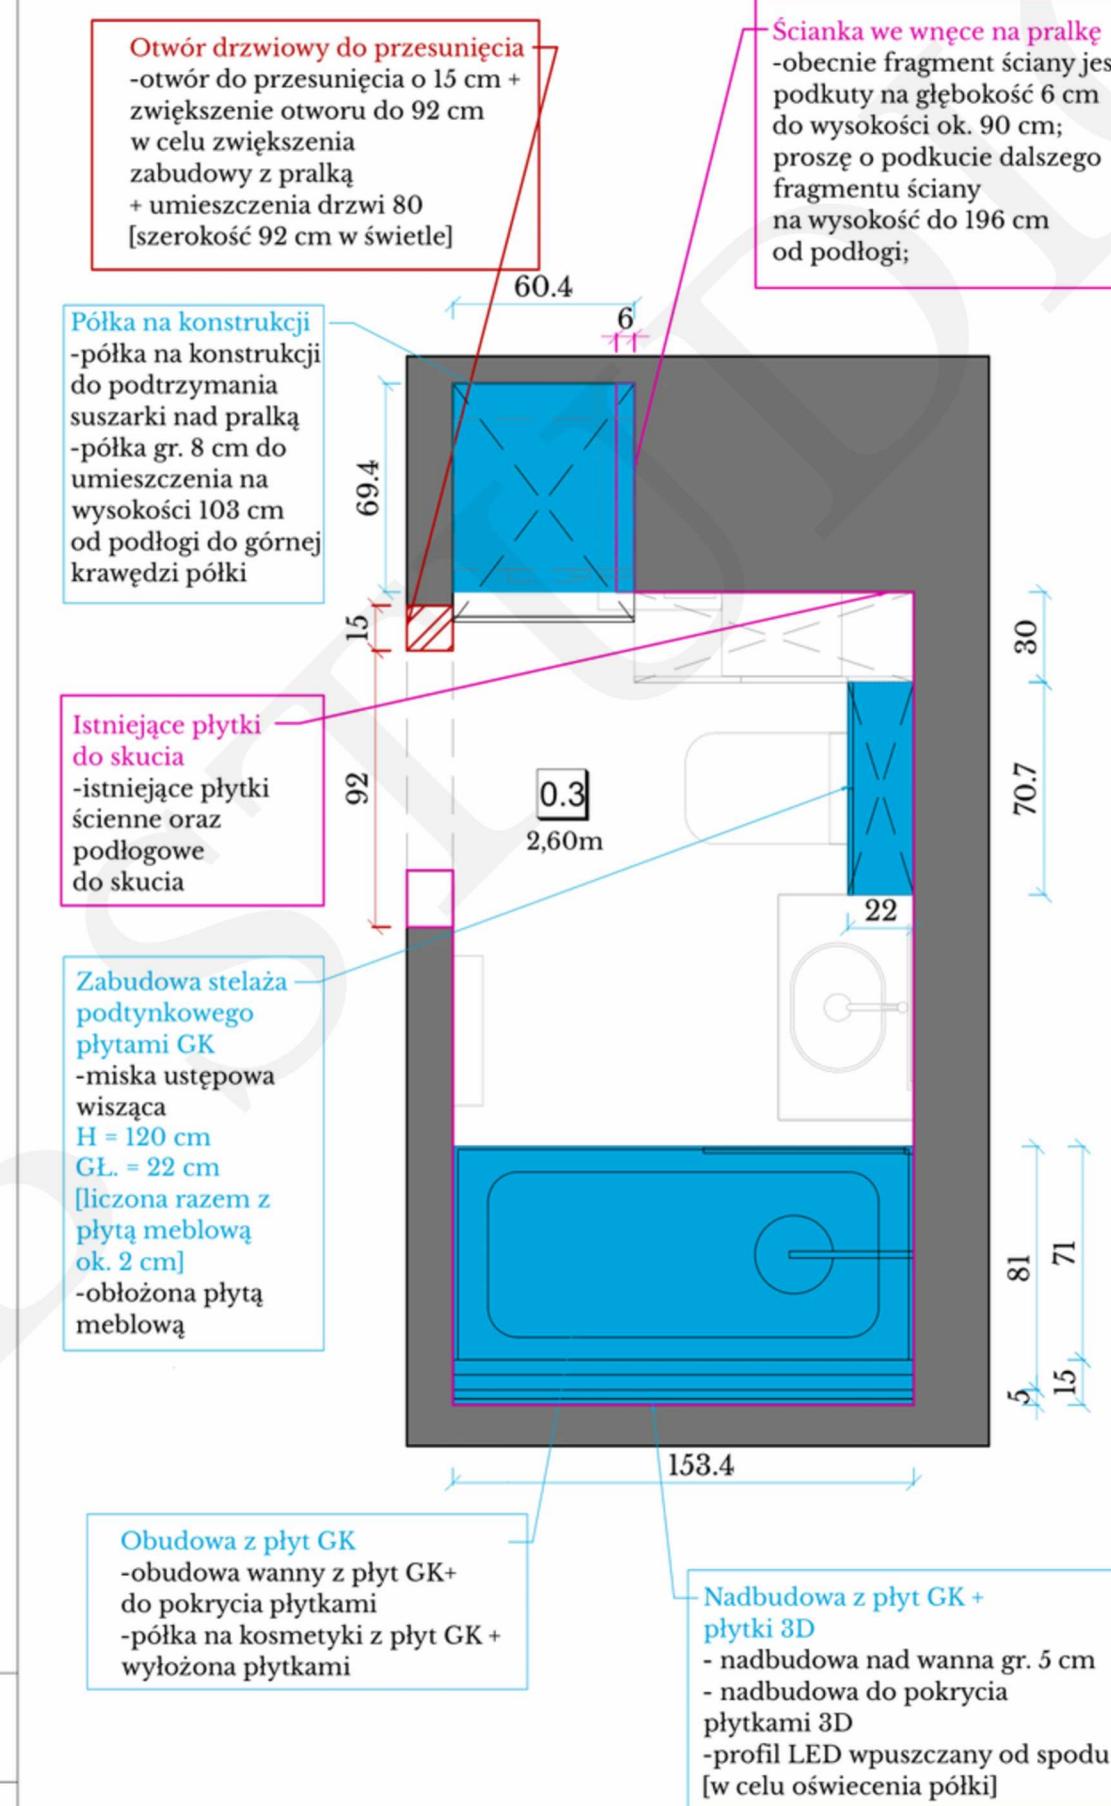

ZESTAWIENIE POWIERZCHNI

NR	NAZWA POMIESZCZENIA	POW. [M ²]
0.01	LAZIENKA	4,57

LEGENDA

	ŚCIANY ISTNIEJĄCE
	ŚCIANY WYBURZENIA
	ELEMENTY PROJEKTOWANE
	SUCHA ZABUDOWA

UWAGI

fugi
Proszę o zastosowanie cienkich fug [2-3mm maksymalnie] + dostosować je jak najbardziej do koloru płyt. Proponowana firma fugi: Fuga Hybrydowa Fugabella Kerakoll

UWAGI

płytka na podłodze
Gres szkliwiony
CR.WELLS IVORY mat
60x120 gat. I
gr. 10,5 mm
Pamesa Ceramica



UWAGI PROJEKTOWE:
1. Przed przystąpieniem do prac należy dokładnie przejrzeć wszystkie rysunki i potwierdzić ich zgodność z Architektem i Inwestorem
2. Wymiary należy sprawdzić na budowie. W momencie wystąpienia widocznych różnic pomiędzy wymiarami na rysunkach, a w rzeczywistości należy skontaktować się z architektem.


Studio
projektowania
wnętrz

K
S T U D I O

NAZWA INWESTYCJI:	PROJEKT WNĘTRZA MIESZKANIA	NUMER RYSUNKU:
ADRES INWESTYCJI:		SKALA RYSUNKU:
INWESTOR:		1:25
LAZIENKA RZUTY PODSTAW. UKŁAD PŁYTEK ZMIANY BUDOWLANE		DATA OPRACOWANIA:
ARCHITEKT: MGR INŻ. ARCH. KAROLINA PLECH TEL.: +48 696 850 891		lipiec 2024.


PRZEKROJE / SUCHA ZABUDOWA / UKŁAD PŁYTEK

PRZEKRÓJ A-A

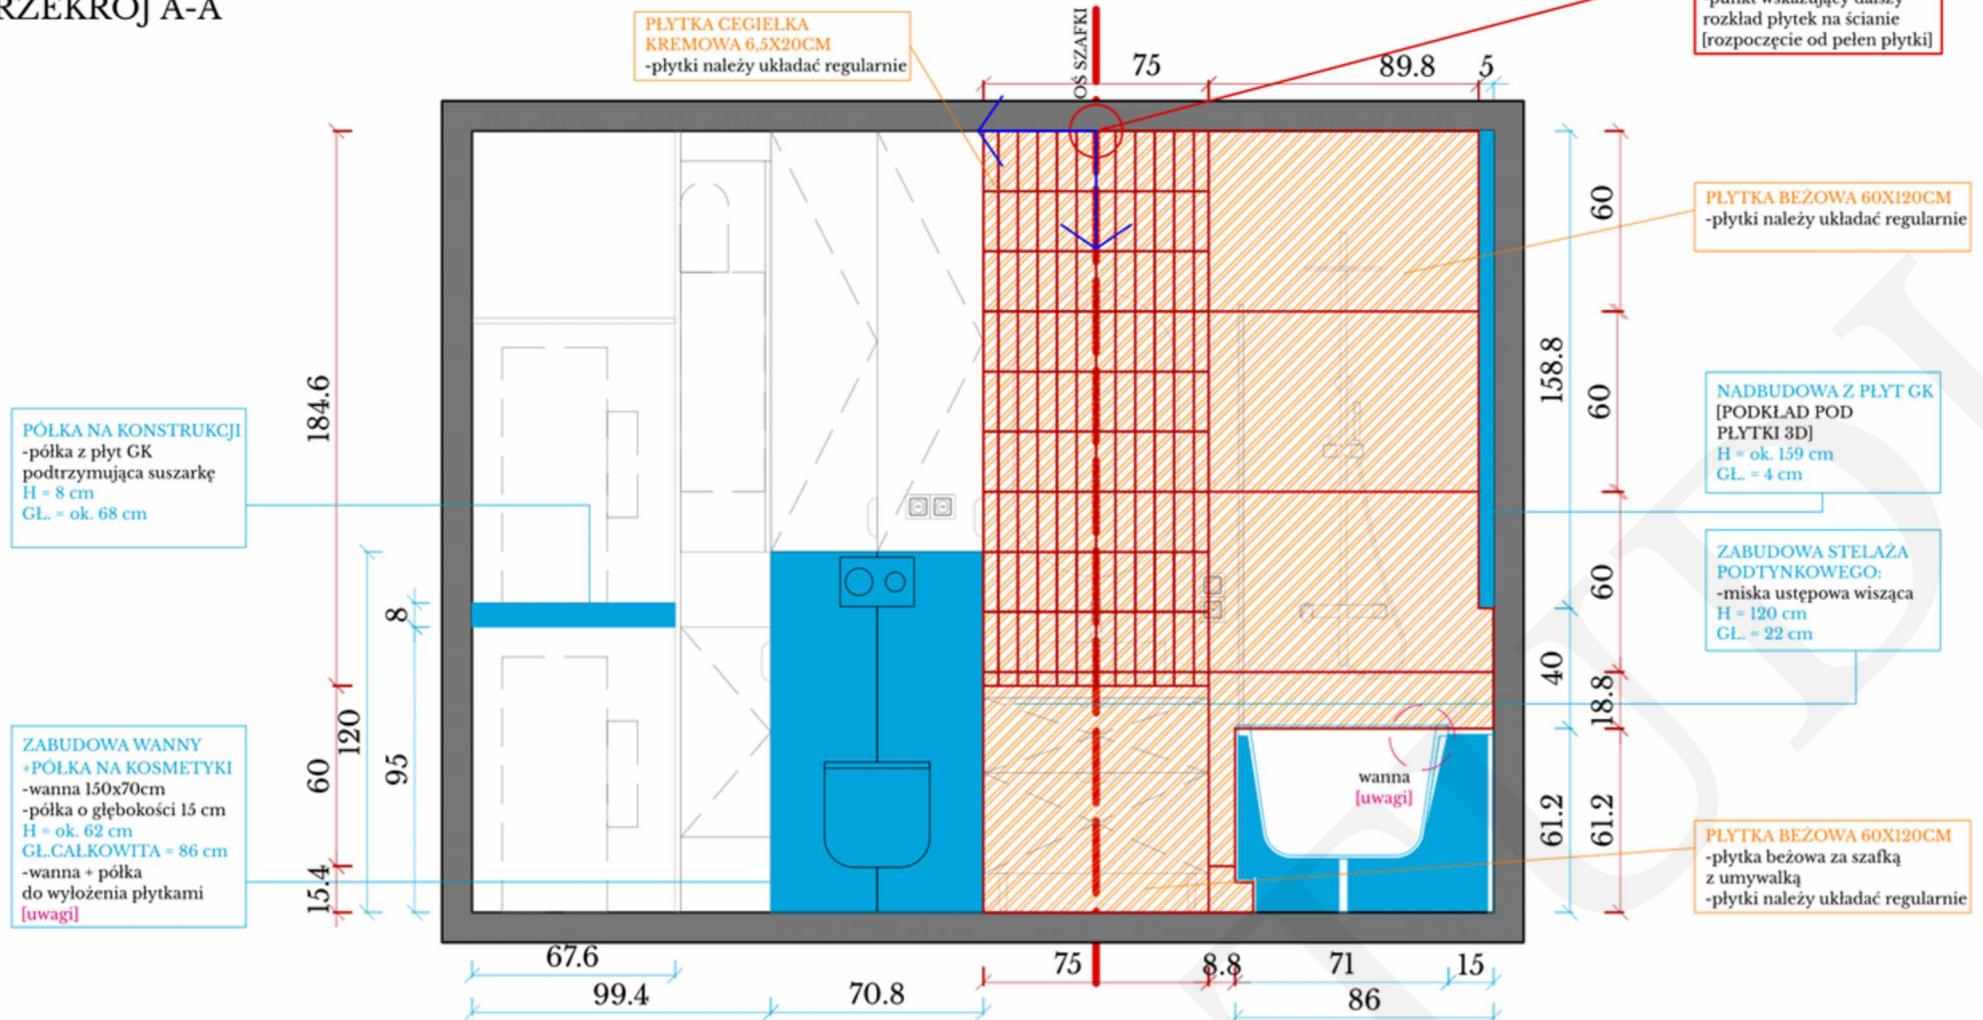


PRZEKROJE / SUCHA ZABUDOWA / UKŁAD PŁYTEK

PRZEKRÓJ B-B

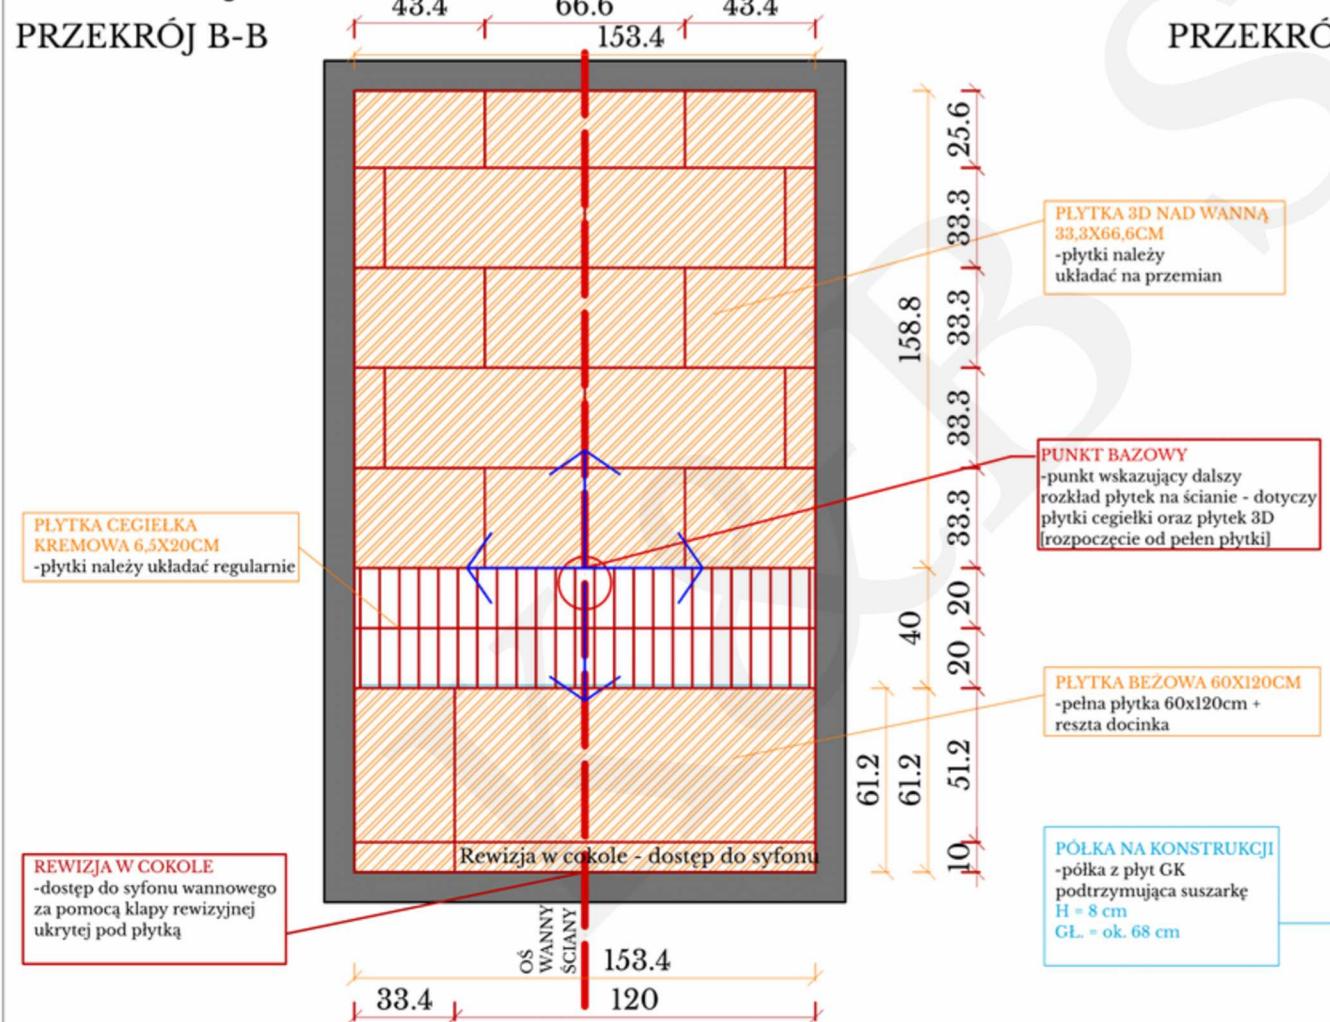

PRZEKRÓJ C-C

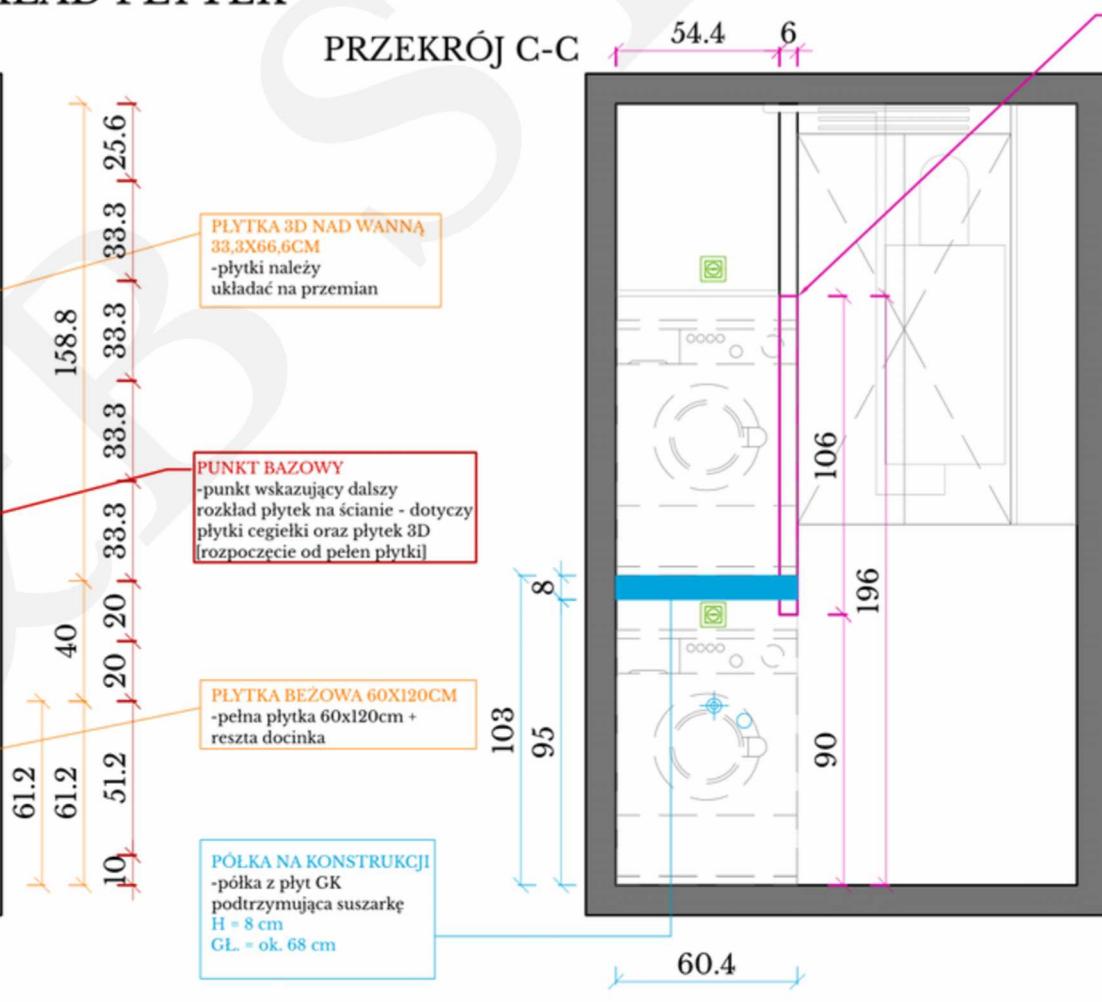


LEGENDA

	ŚCIANY ISTNIEJĄCE
	ŚCIANY WYBURZENIA
	SUCHA ZABUDOWA
	PŁYTKI UKŁAD
	FUGA

MATERIAŁY [UWAGI]

płytki 3D nad wanną
Płytki ścienne hiszpańska BOLSOI COBRE 33,3x66,6 gat. I gr.10,5 mm El Molino

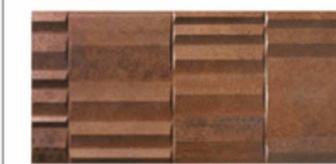

płytki za lustrem + we wnęce na kosmetyki [półka za wanną]
ARTISAN OCHRE kremowa 20x6,5 cm gr. 9 mm EQUIPE



płytki za prysznicem + na podłodze + obudowa wanny + półka na kosmetyki
Gres szkliwiony CR.WELLS IVORY mat 60x120 gat. I gr. 10,5 mm Pamesa Ceramica



UWAGI

FUGI

Proszę o zastosowanie cienkich fug [2-3mm maksymalnie] + dopasować je jak najbardziej do koloru płyt. Proponowana firma fug: Fuga Hybrydowa Fugabella Kerakoll

WANNA

Zabudowa została dostosowana do wanny: Koło Opal Plus wanna prostokątna 150x70 cm biała XWP1250000


Studio projektowania wnętrz

K
S T U D I O


NAZWA INWESTYCJI:	PROJEKT WNĘTRZA MIESZKANIA	NUMER RYSUNKU:
ADRES INWESTYCJI:		SKALA RYSUNKU:
INWESTOR:		1:25
LAZIENKA SUCHA ZABUDOWA UKŁADY WYKOŃ. ŚCIAN		DATA OPRACOWANIA:
		lipiec 2024 r.
ARCHITEKT:	MGR INŻ. ARCH. KAROLINA PLECH TEL.: + 48 696 850 891	

PRZEKROJE / ARANŻACJA / WOD KAN

PRZEKROJ C-C 153.4

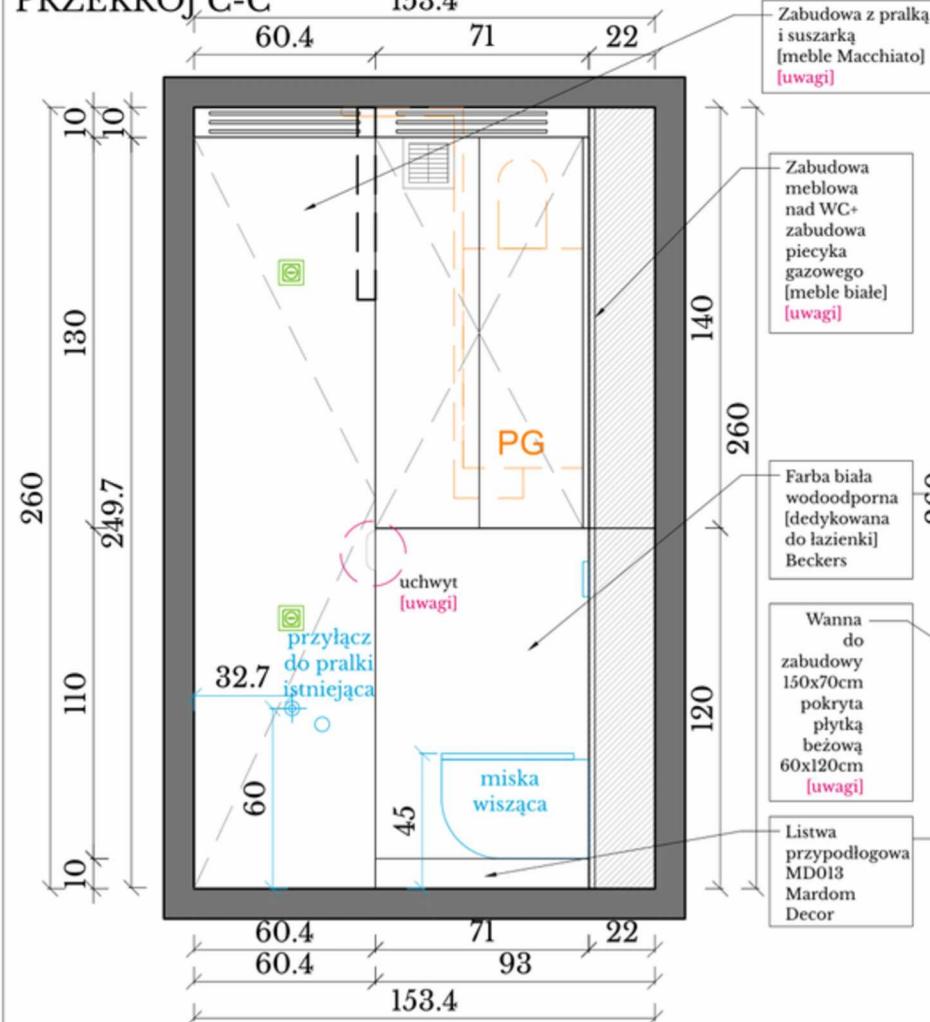

PRZEKROJ D-D

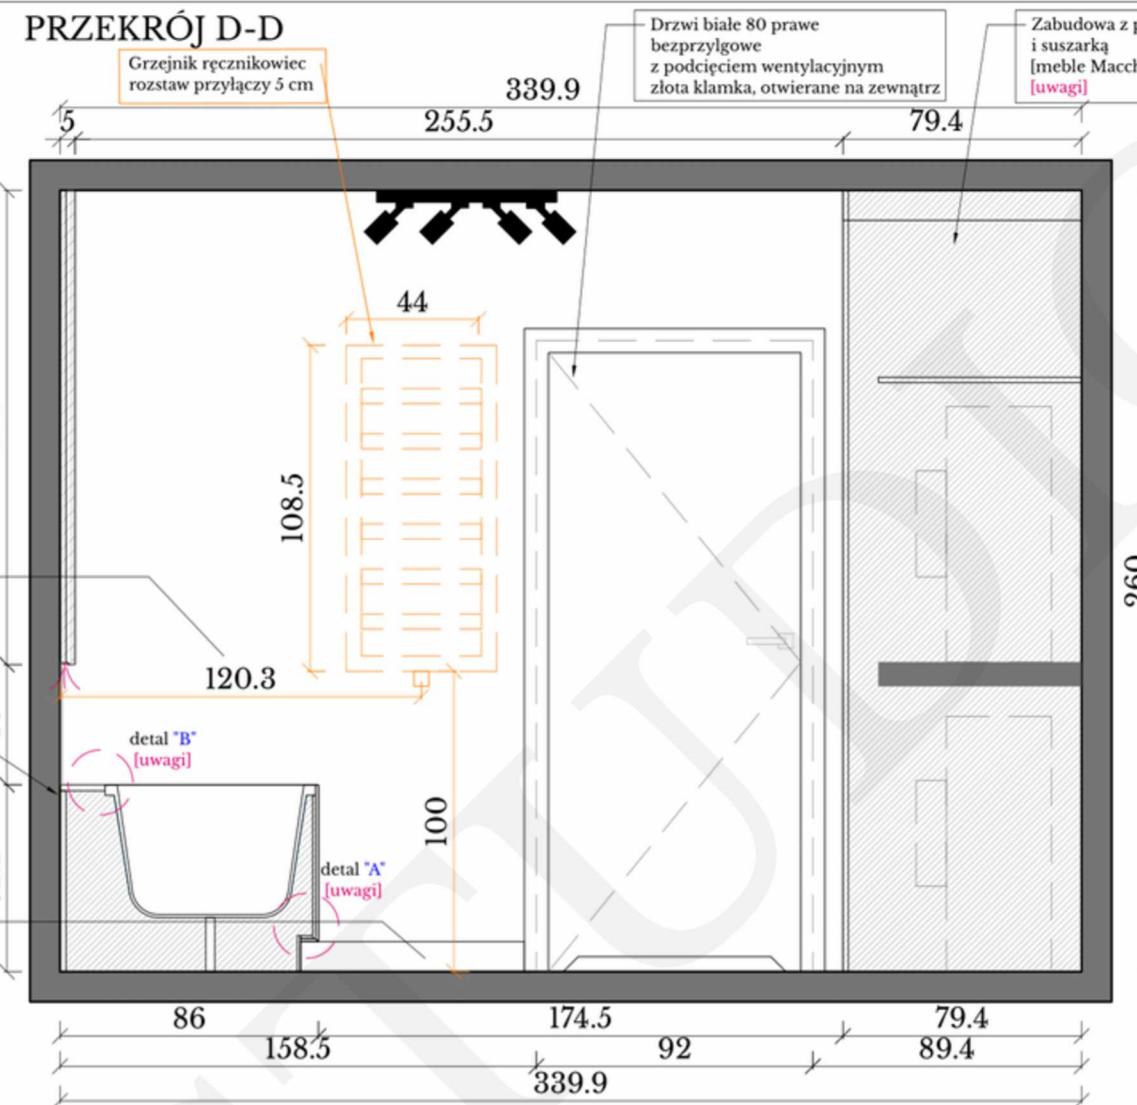

LEGENDA

ŚCIANY ISTNIEJĄCE

PRZEKRÓJ PRZEZ MEBLE / ZABUDOWĘ

LUSTRO

MATERIAŁY [UWAGI]

plytka 3D nad wanną
Płytki ścienne hiszpańska
BOLSOI COBRE
33,3x66,6 gat. I
gr.10,5 mm
El Molino



plytka za lustrem + we wnęce
na kosmetyki [półka za wanną]
ARTISAN OCHRE kremowa
20x6,5 cm
gr. 9 mm
EQUIPE



plytka za prysznicem + na podłodze + obudowa wanny
Gres szkliwiony
CR.WELLS IVORY mat

60x120 gat. I
gr. 10,5 mm
Pamesa Ceramica

Meble Macchiato

fronty + boki

widoczne

płyta laminowana

Macchiato 8533 BS

ZŁOTY

wymiar: 130 mm

HVYT

Meble biale

fronty + boki

widoczne

płyta laminowana

Macchiato 8533 BS

ZŁOTY

wnętrze

płyta laminowana

biała

Uchwyt krawędziowy

Uchwyt ELMO

ZŁOTY


wymiar: 130 mm

HVYT

DETALE [UWAGI]

"A"

łączenie płytek
pod kątem 45 stopni

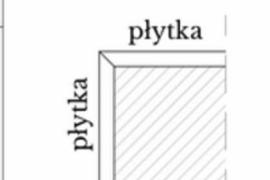

"B"

zlicowanie rantu wanny
z półką na kosmetyki
we wnęce




UWAGI PROJEKTOWE:


- Przed przystąpieniem do prac należy dokładnie przejrzeć wszystkie rysunki i potwierdzić ich zgodność z Architektem i Inwestorem
- Wymiary należy sprawdzić na budowie. W momencie wystąpienia widocznych różnic pomiędzy wymiarami na rysunkach, a w rzeczywistości należy skontaktować się z architektem.

PRZEKROJE / INSTALACJE ELEKTRYCZNE

PRZEKROJ C-C

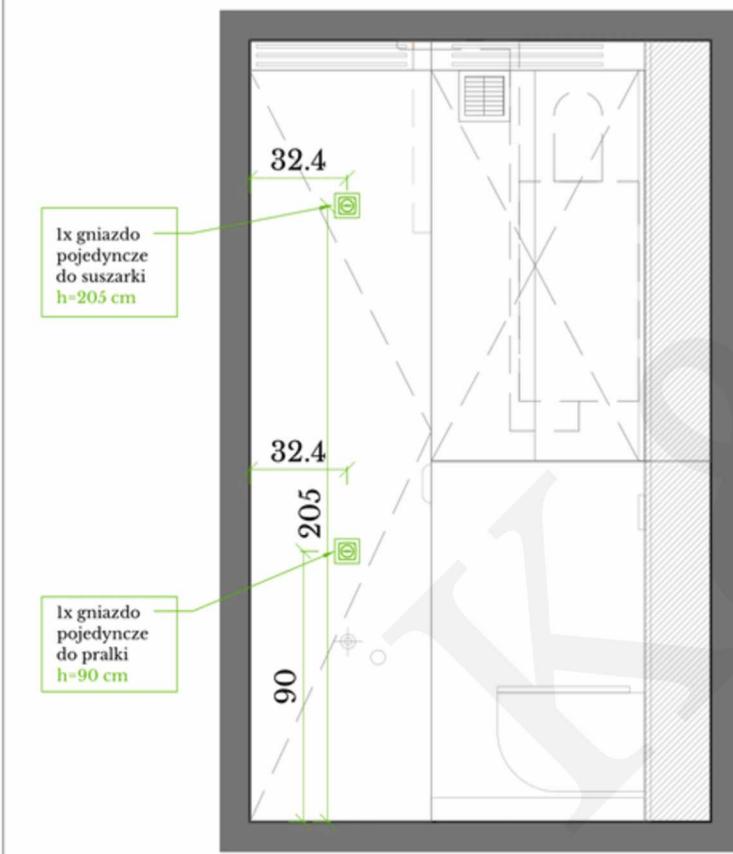

PRZEKROJ D-D

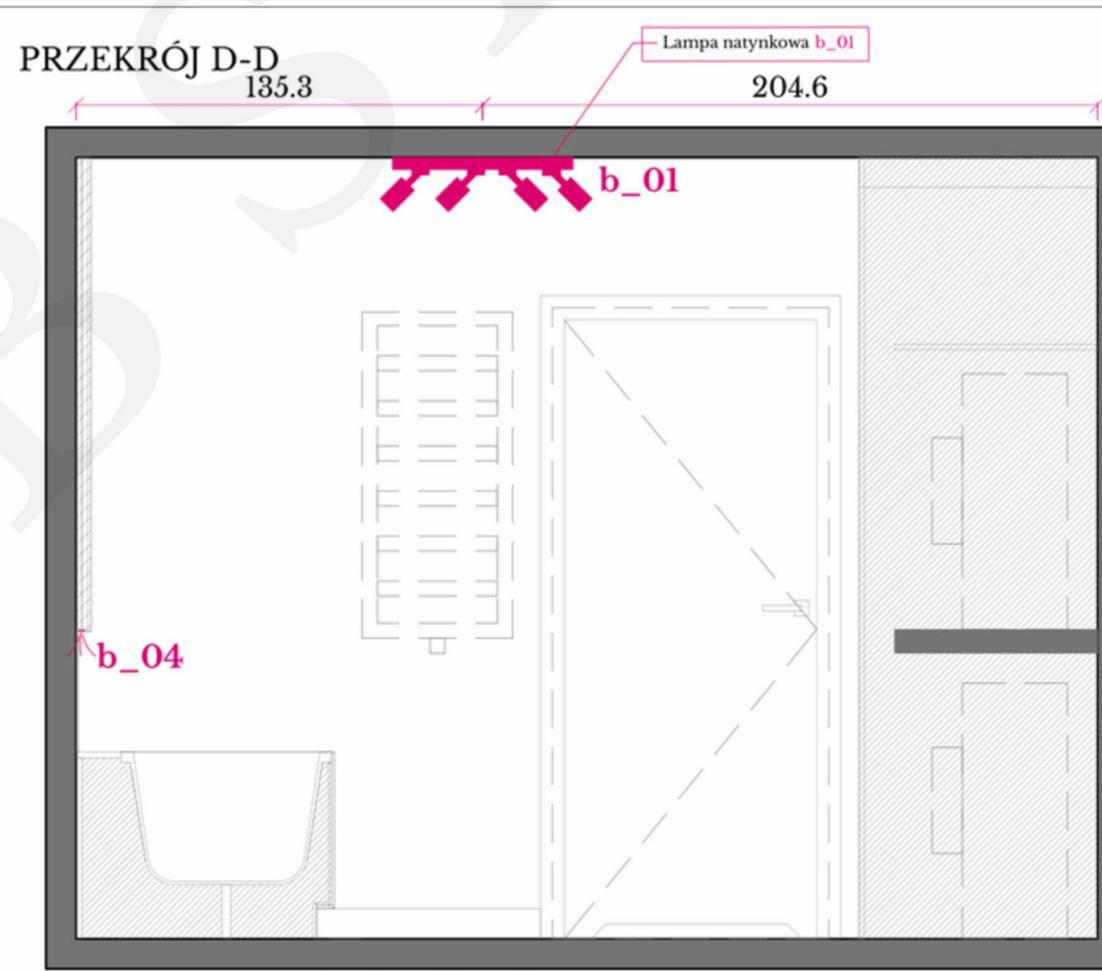


Studio
projektowania
wnętrz

K
S T U D I O

NAZWA INWESTYCJI:	PROJEKT WNĘTRZA MIESZKANIA	NUMER RYSUNKU:
ADRES INWESTYCJI:		SKALA RYSUNKU:
INWESTOR:		1:25
LAZIENKA PRZEKRÓJ C-C,D-D		DATA OPRACOWANIA:
ARANŻACJA INSTALACJE ELEKTRYCZNE		lipiec 2024r.
ARCHITEKT:	MGR INŻ. ARCH. KAROLINA PLECH TEL.: +48 696 850 891	

RYSUNKI DLA STOLARZA RYS. 1 [ŁAZIENKA]

SZAFKA Z UMYWALKĄ + ZABUDOWA Z PRALKĄ + ZABUDOWA BEZ DNA ZAKRYWAJĄCA PIECYK GAZOWY + SZAFKA NAD WC

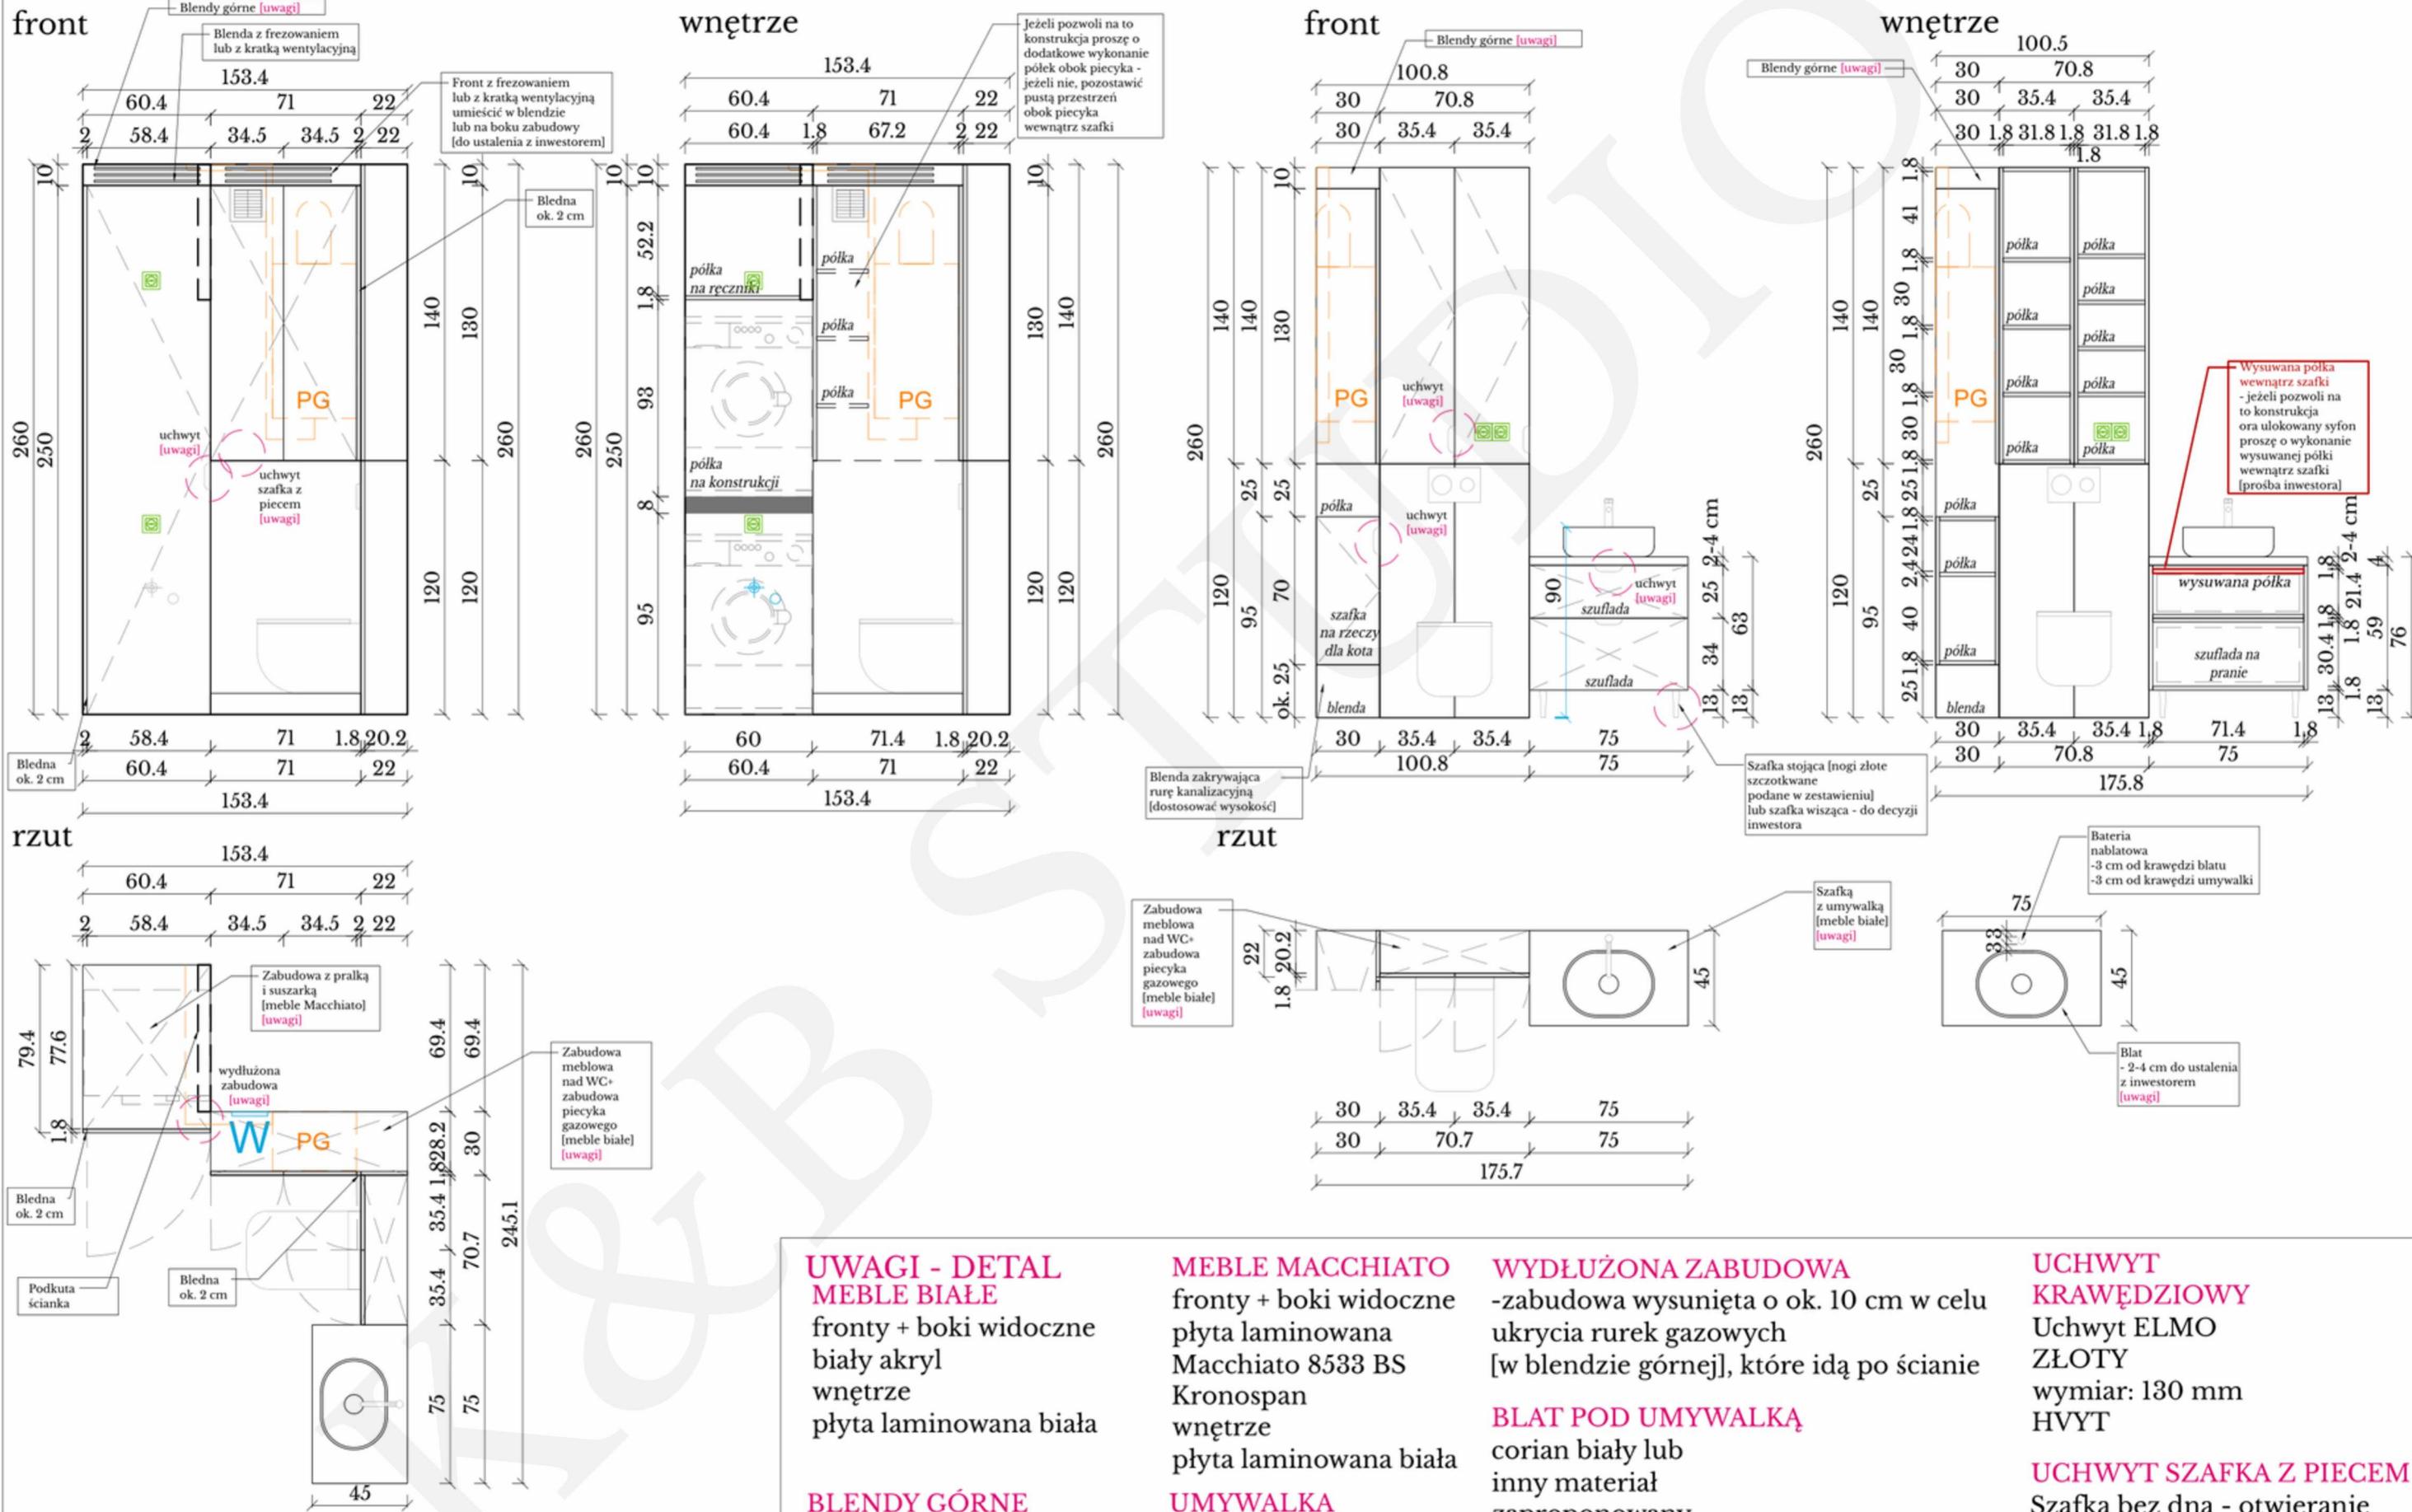



K&B

K & B STUDIO
projektowanie
wnętrz



K
B

K & B STUDIO
projektowanie
wnętrz